
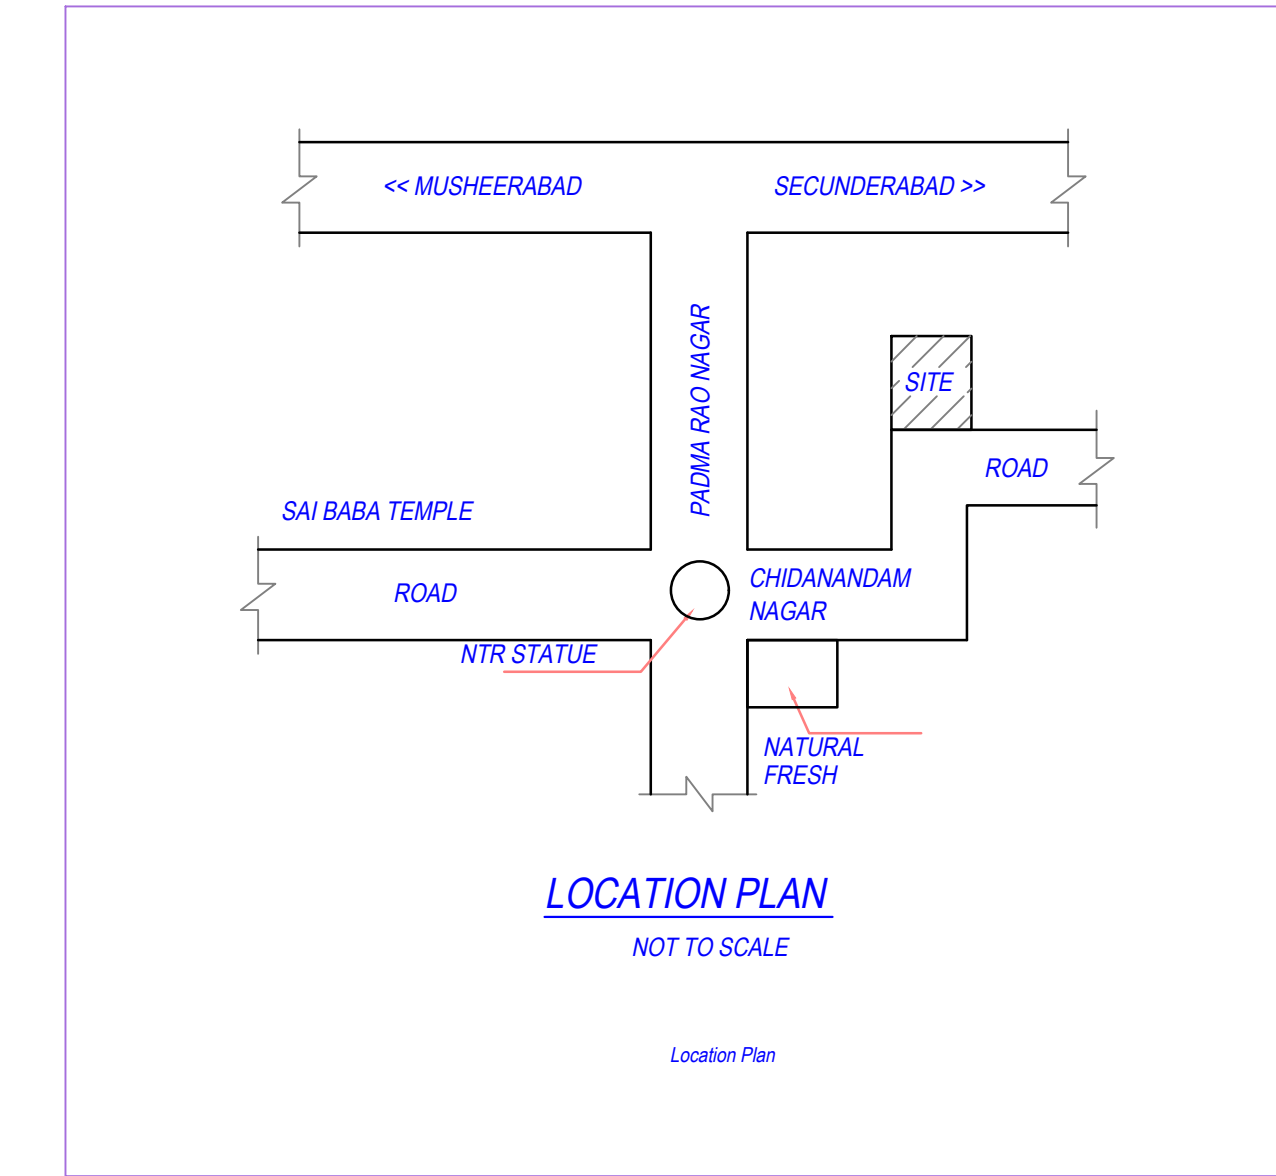


Project Title :PLAN SHOWING THE PROPOSED RESIDENTIAL FLATS ON HOUSE No. 6-1-276/A/3, 6-1-276/A/3/1, 6-1-276/A/3/2, 6-1-276/A/3/3 AND6-1-276/A/3/4 AT PADMA RAO NAGAR, SECUNDERABAD.BELONGS TO :M/s. RUBRICON INFRA Represented by its Managing Partners:1. Smt. MOLLASRI SAMUDRALA, W/o. Sri. RAMESH SAMUDRALA,2. Sri. B. GOVARDHANA CHARY, S/o. Sri. B. LAXMANA CHARY.







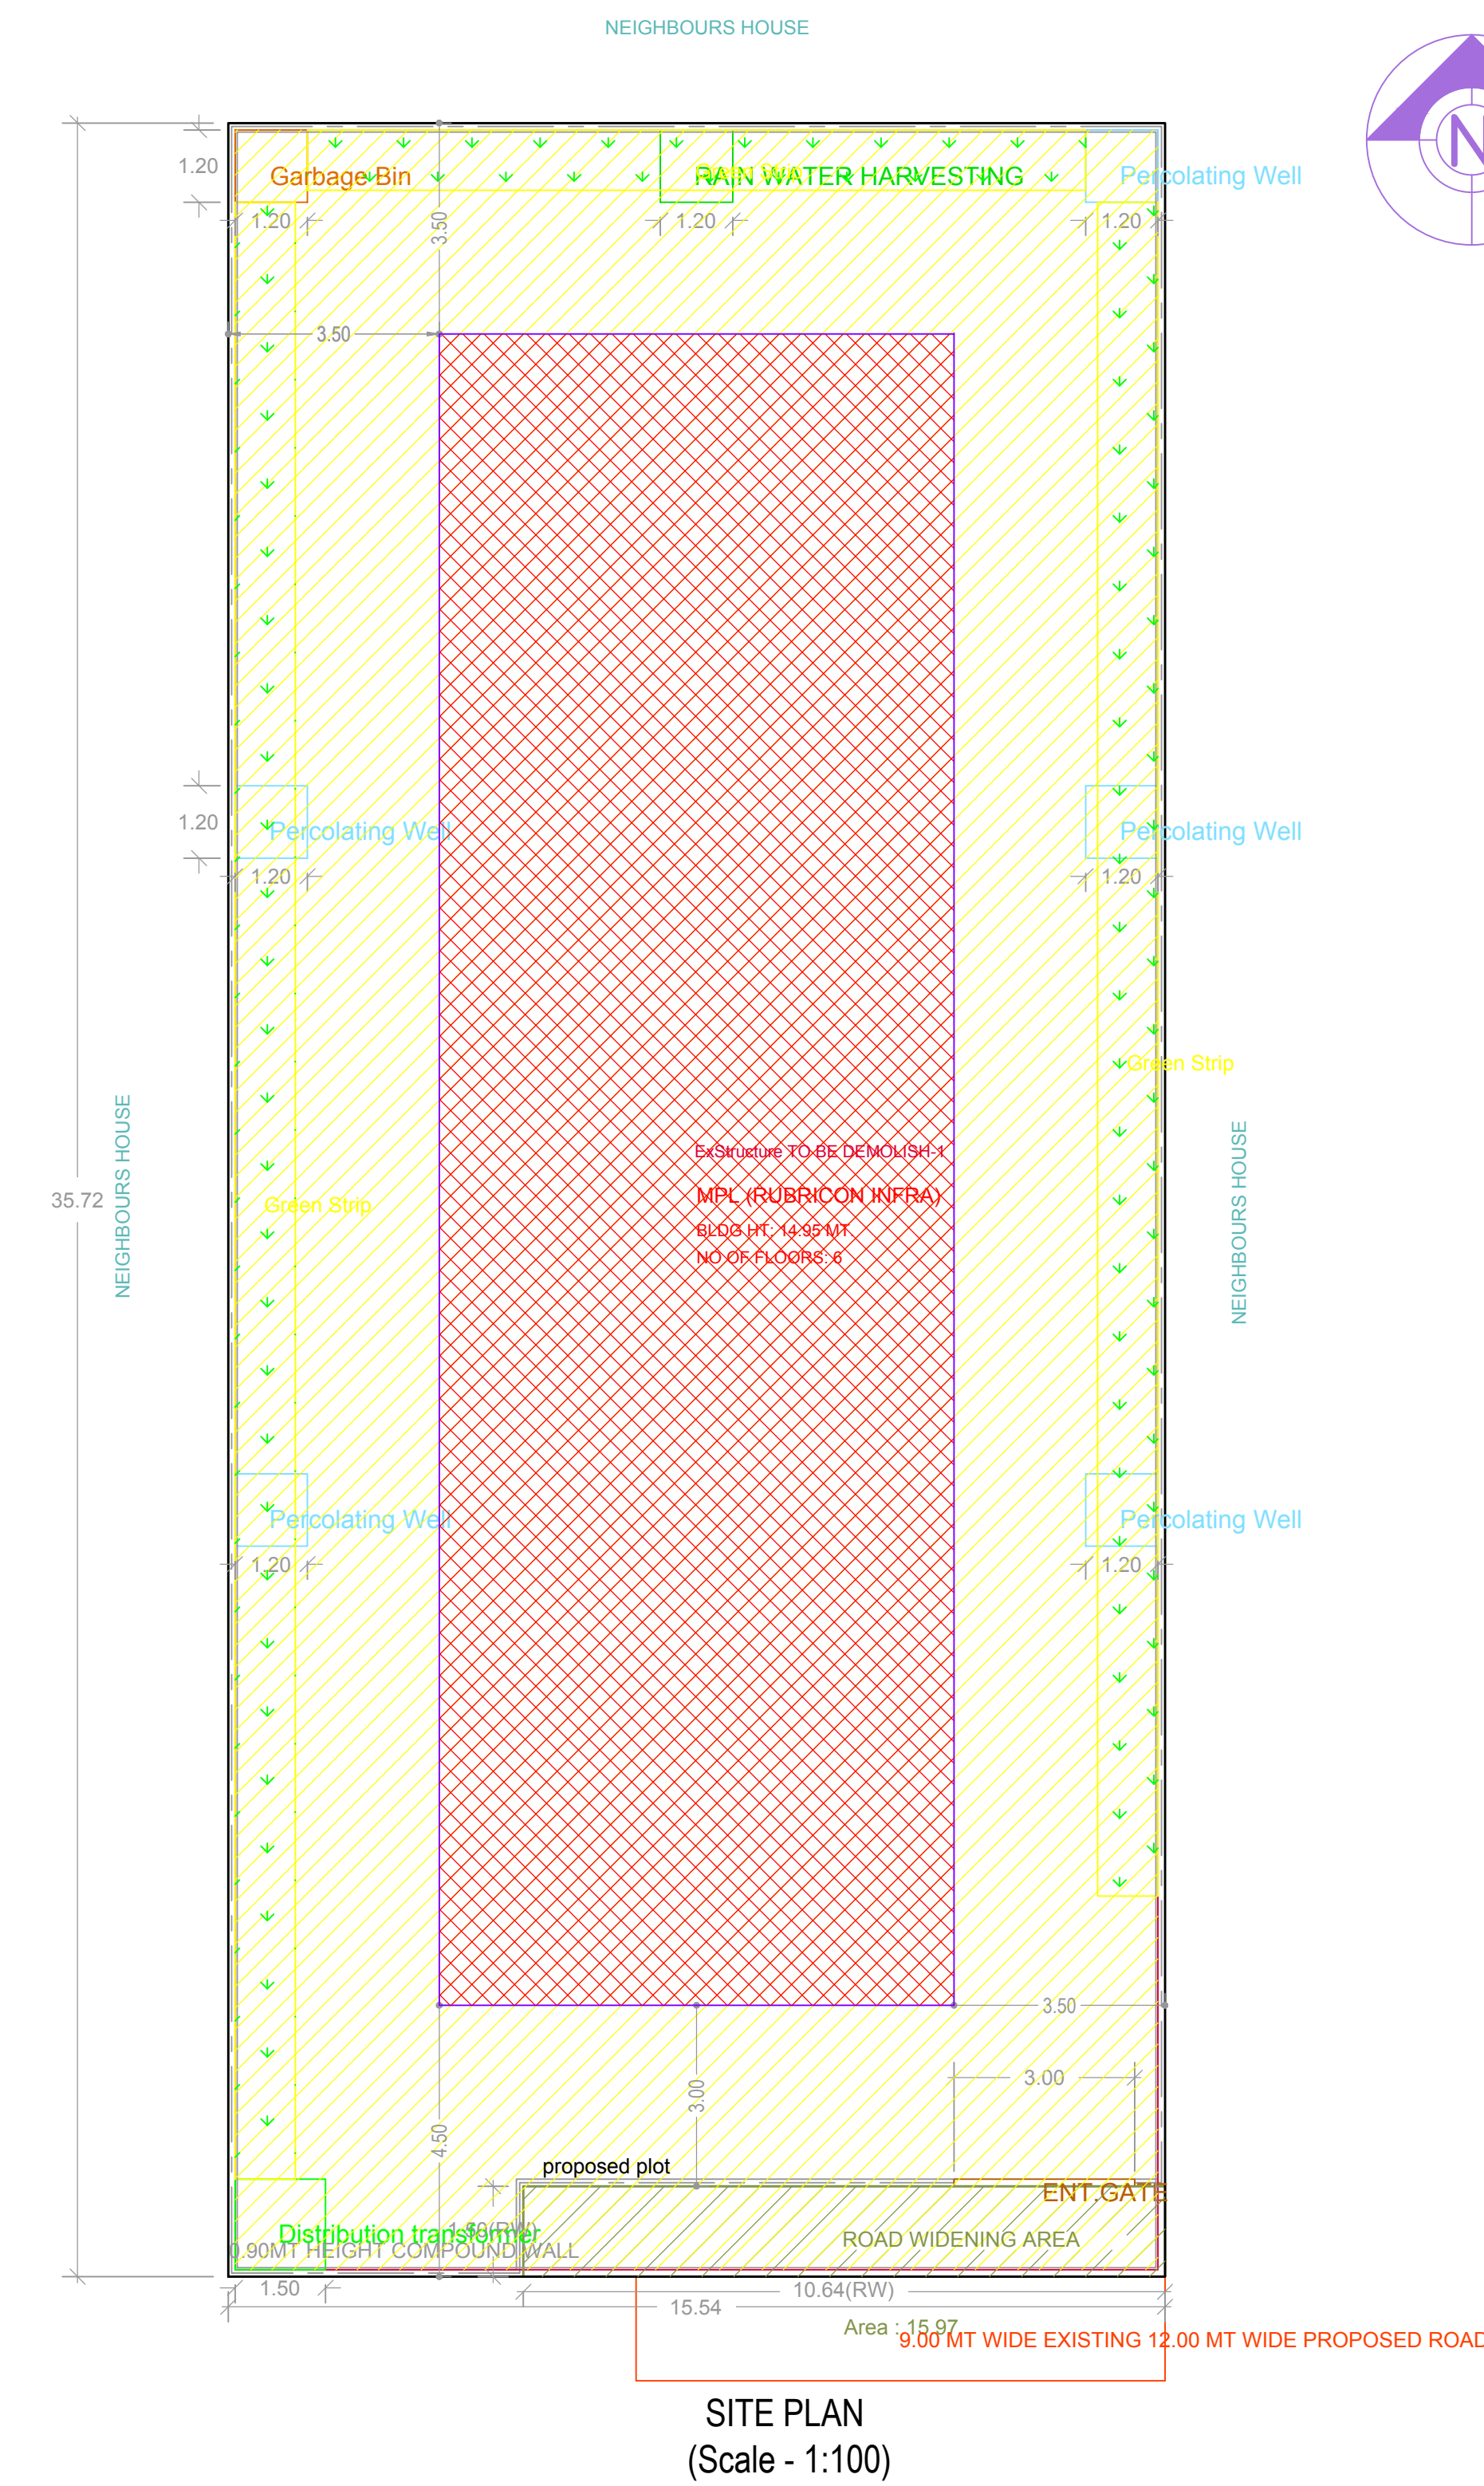


BUILDING -MPL (RUBRICON INFRA)						
FLOOR NAME	TOTAL BUA	NET BUA	THMTS.	PARKING AREA	NO OF STICK	NET PARKING
PARKING FLOOR	236.70	0.00	00	236.70	1	236.70
FIRST FLOOR	236.73	236.73	02	0.00	0	0.00
SECOND FLOOR	236.73	236.73	02	0.00	0	0.00
THIRD FLOOR	236.73	236.73	02	0.00	0	0.00
FOURTH FLOOR	236.73	236.73	02	0.00	0	0.00
FIFTH FLOOR	236.73	236.73	02	0.00	0	0.00
TERRACE FLOOR	2.25	0.00	00	0.00	0	0.00
TOTAL	1422.60	1183.65	10	236.70	236.70	10.71
TOTAL NO OF BLDG	1					
TOTAL	1422.60	1183.65	10	236.70	236.70	10.71

Balcony Calculations Table			
FLOOR NAME	SIZE	TOTAL AREA	
TYPICAL - 2, 3, 4 & 5 FLOOR PLAN	1.70 X 3.81 X 1.4	42.84	
FIRST FLOOR PLAN	1.25 X 3.39 X 1.4	10.71	
Total	1.25 X 3.39 X 1	53.55	

SCHEDULE OF JOINERY			
BUILDING NAME	NAME	L X H	NOS
MPL (RUBRICON INFRA)	D2	0.75 X 2.10	35
MPL (RUBRICON INFRA)	D1	0.90 X 2.10	40
MPL (RUBRICON INFRA)	OPEN	1.02 X 2.10	05
MPL (RUBRICON INFRA)	MD	1.05 X 2.10	10
MPL (RUBRICON INFRA)	WD	1.52 X 2.10	05
MPL (RUBRICON INFRA)	OPEN	2.98 X 2.10	05


SCHEDULE OF JOINERY			
BUILDING NAME	NAME	L X H	NOS
MPL (RUBRICON INFRA)	W	0.90 X 0.90	25
MPL (RUBRICON INFRA)	W1	1.41 X 1.50	05
MPL (RUBRICON INFRA)	KW	1.50 X 1.00	10
MPL (RUBRICON INFRA)	W1	1.50 X 1.50	40
MPL (RUBRICON INFRA)	W	1.71 X 1.50	01
MPL (RUBRICON INFRA)	W	1.80 X 1.50	04
MPL (RUBRICON INFRA)	W0	2.10 X 1.50	10

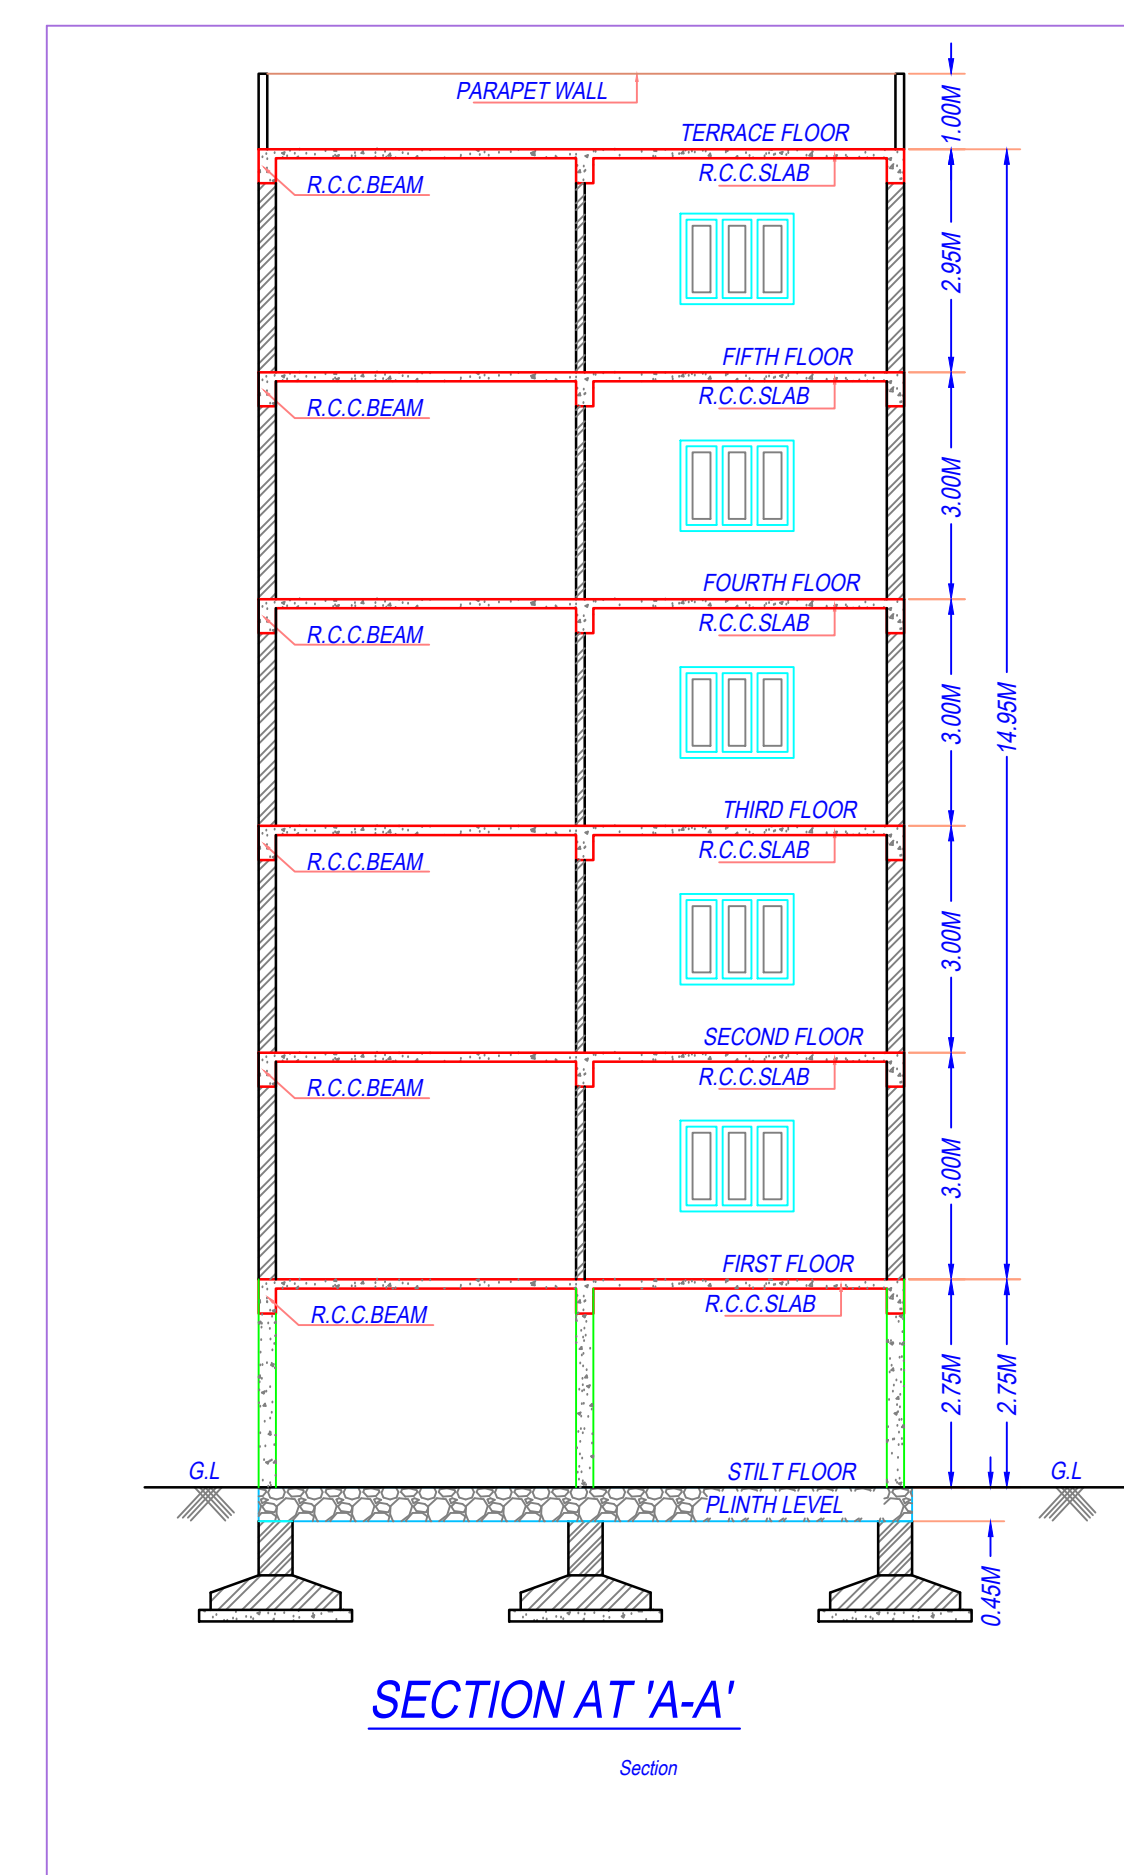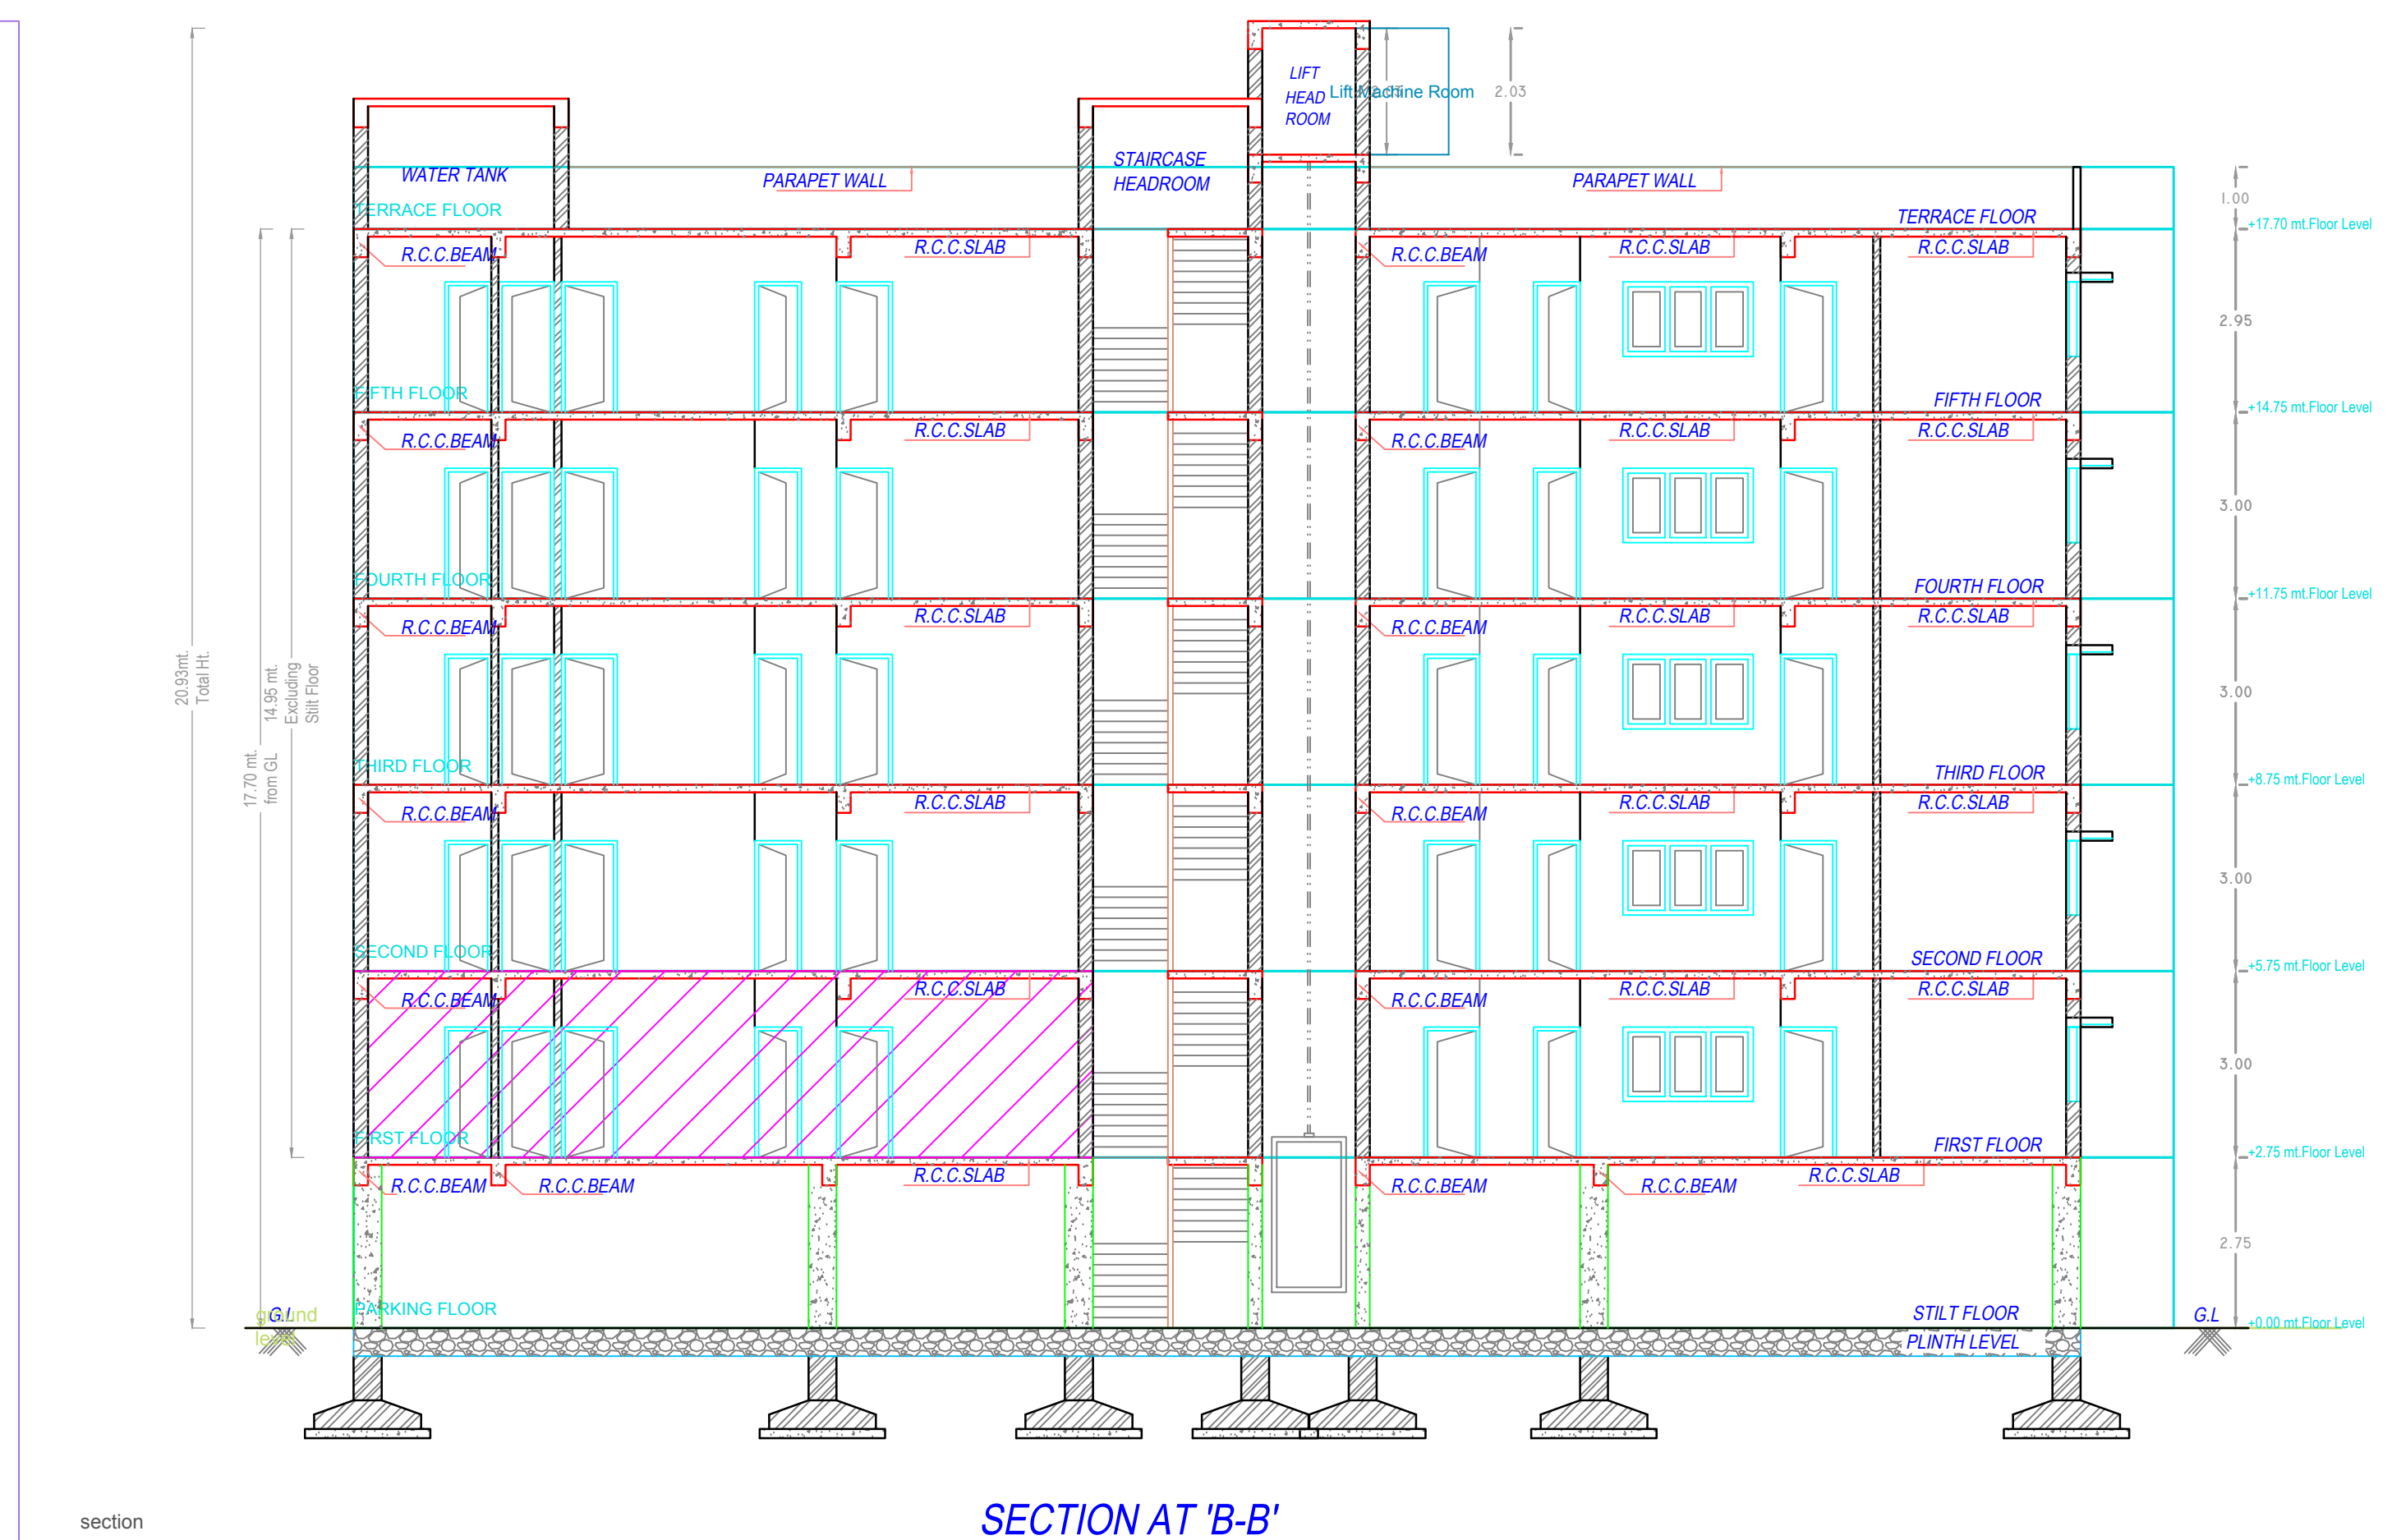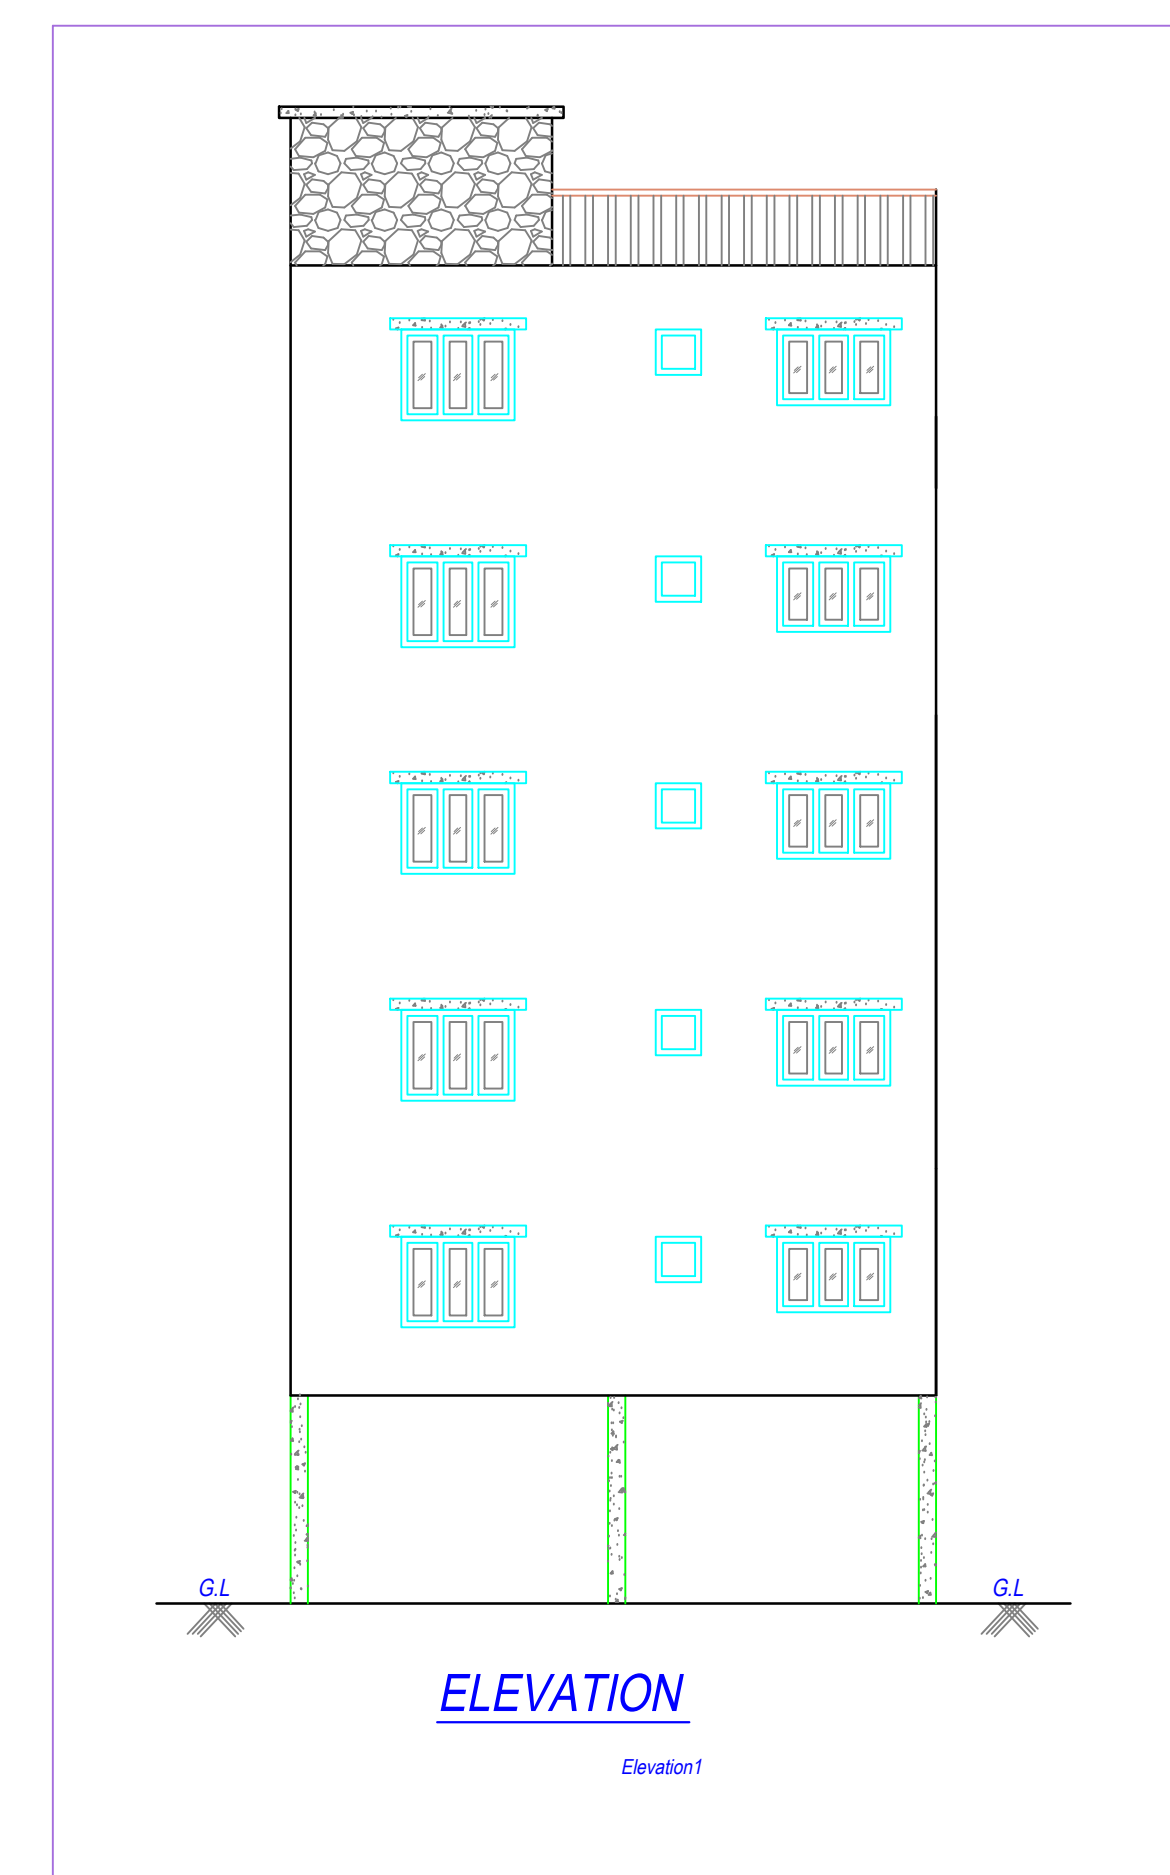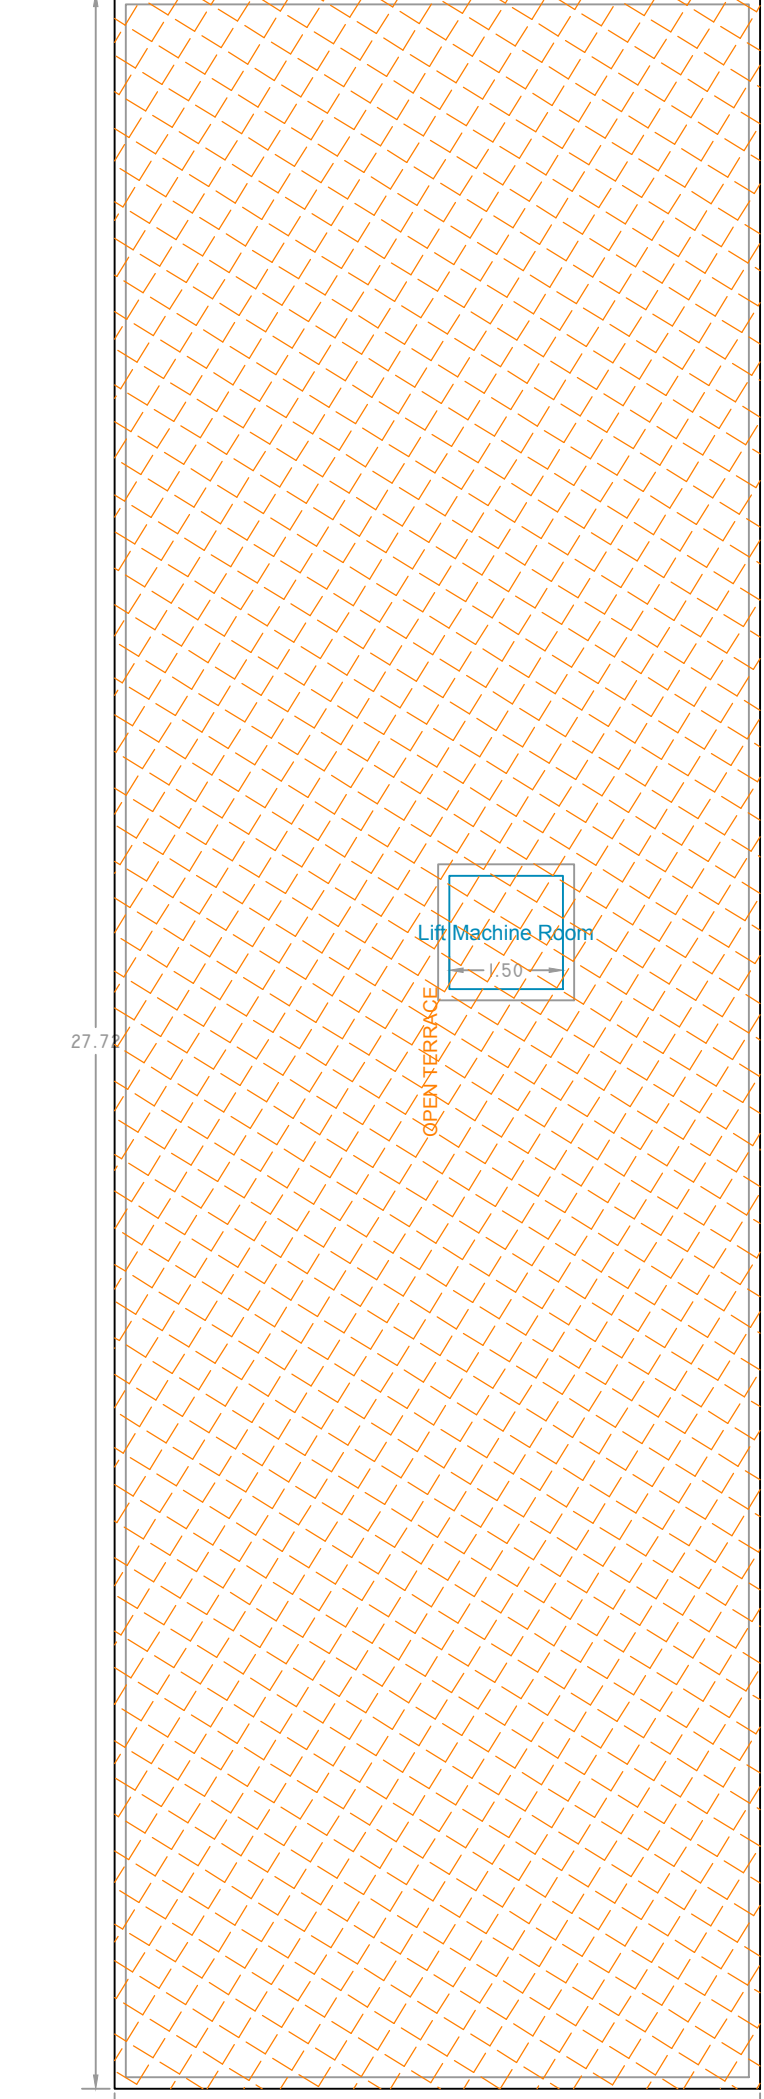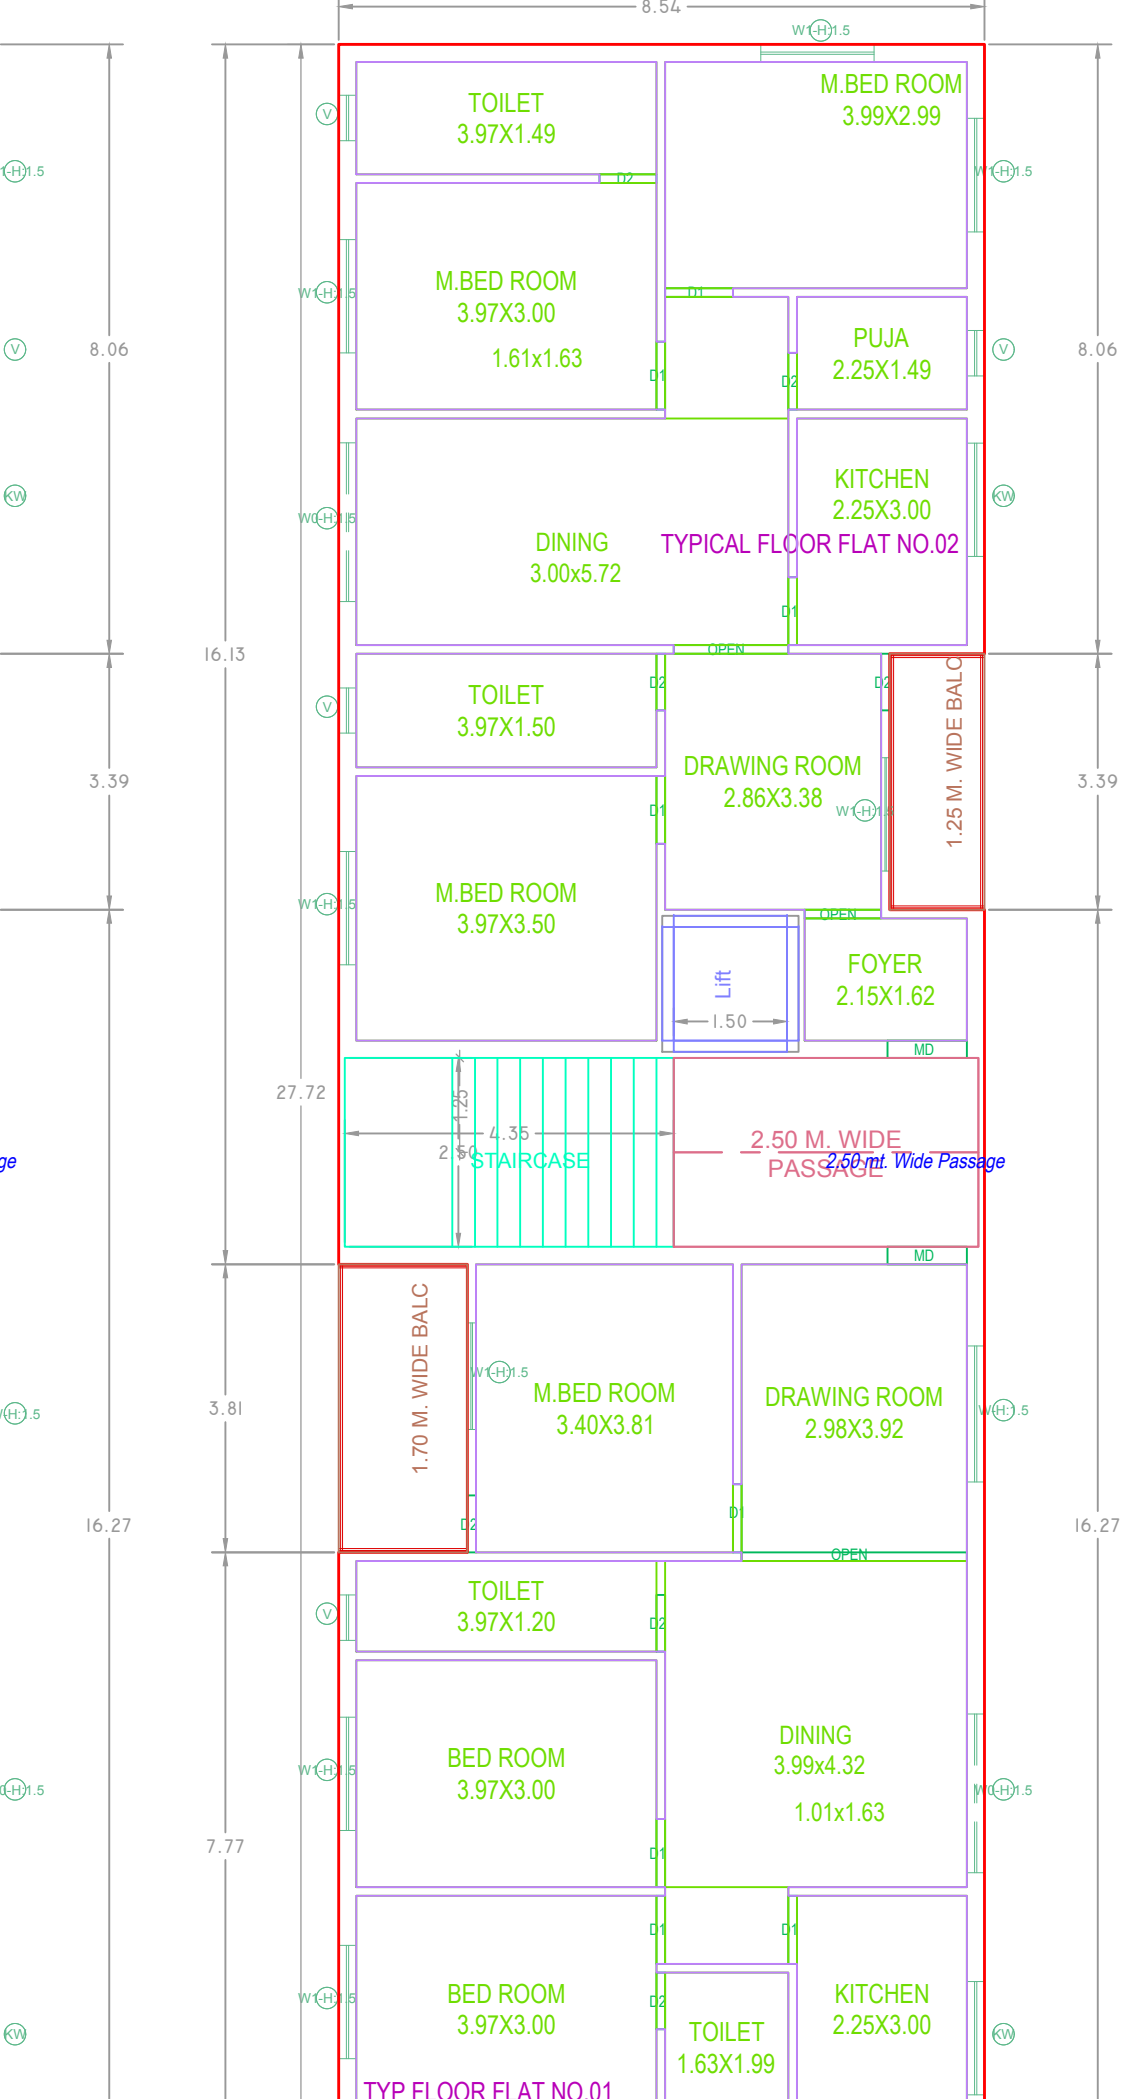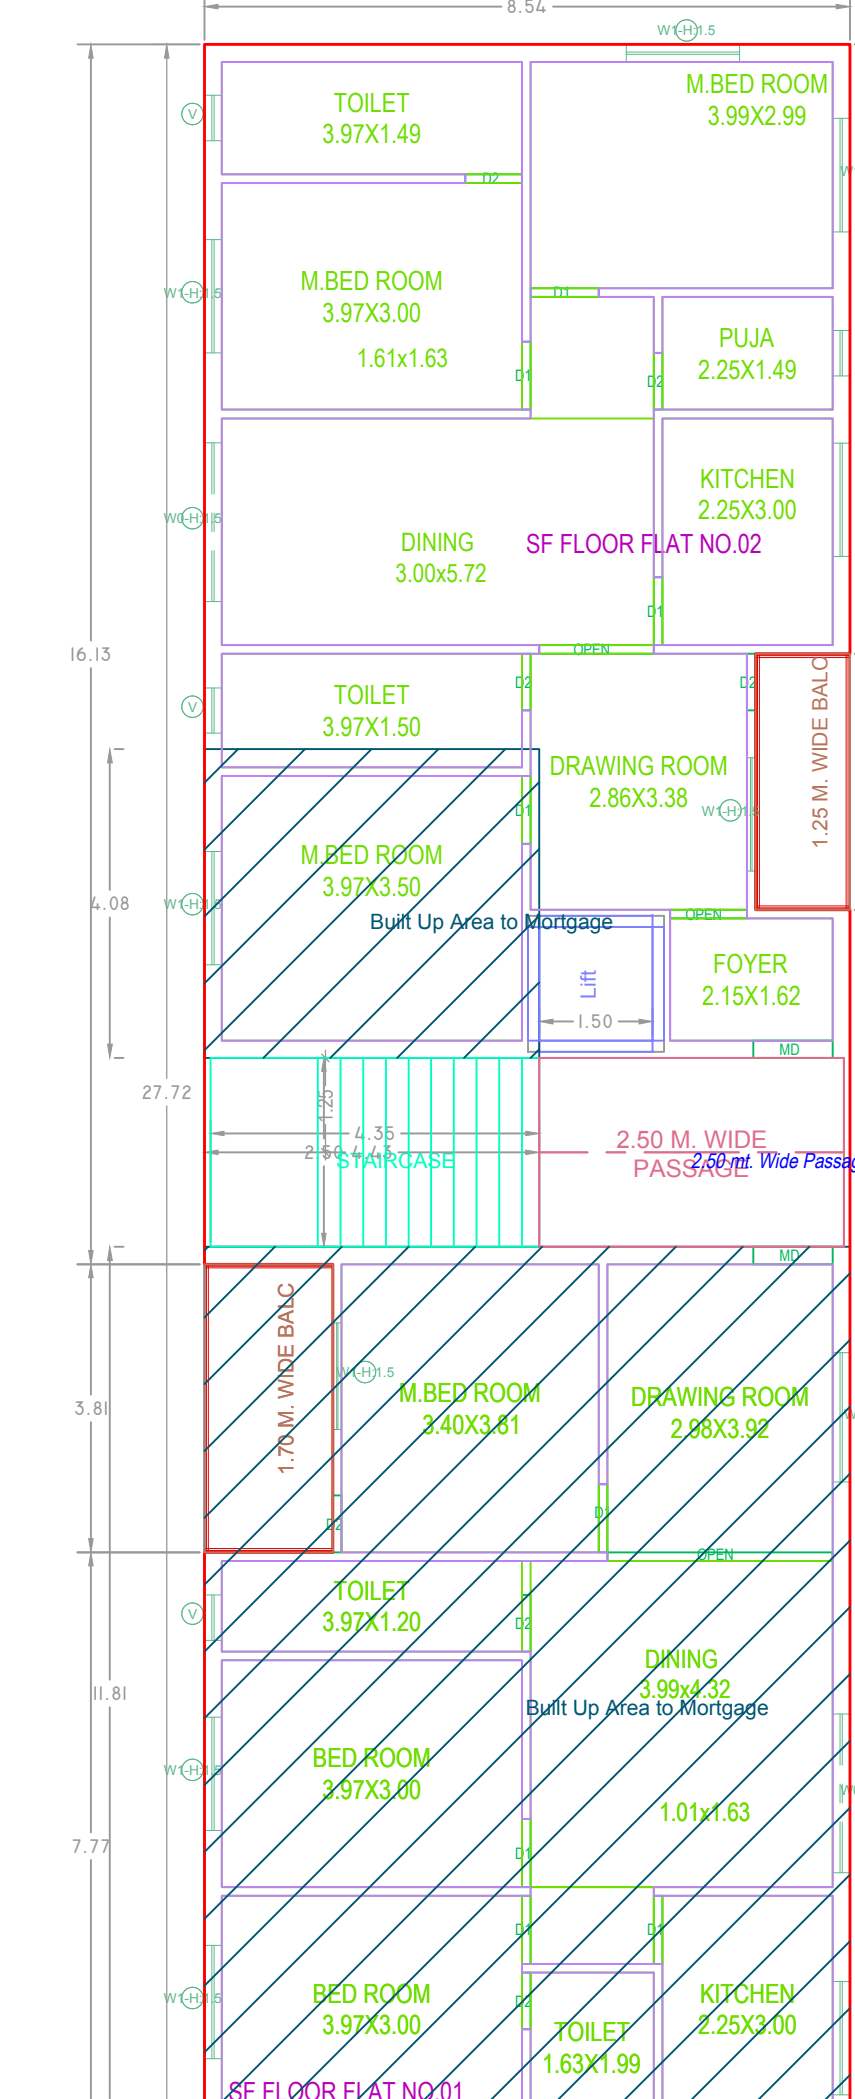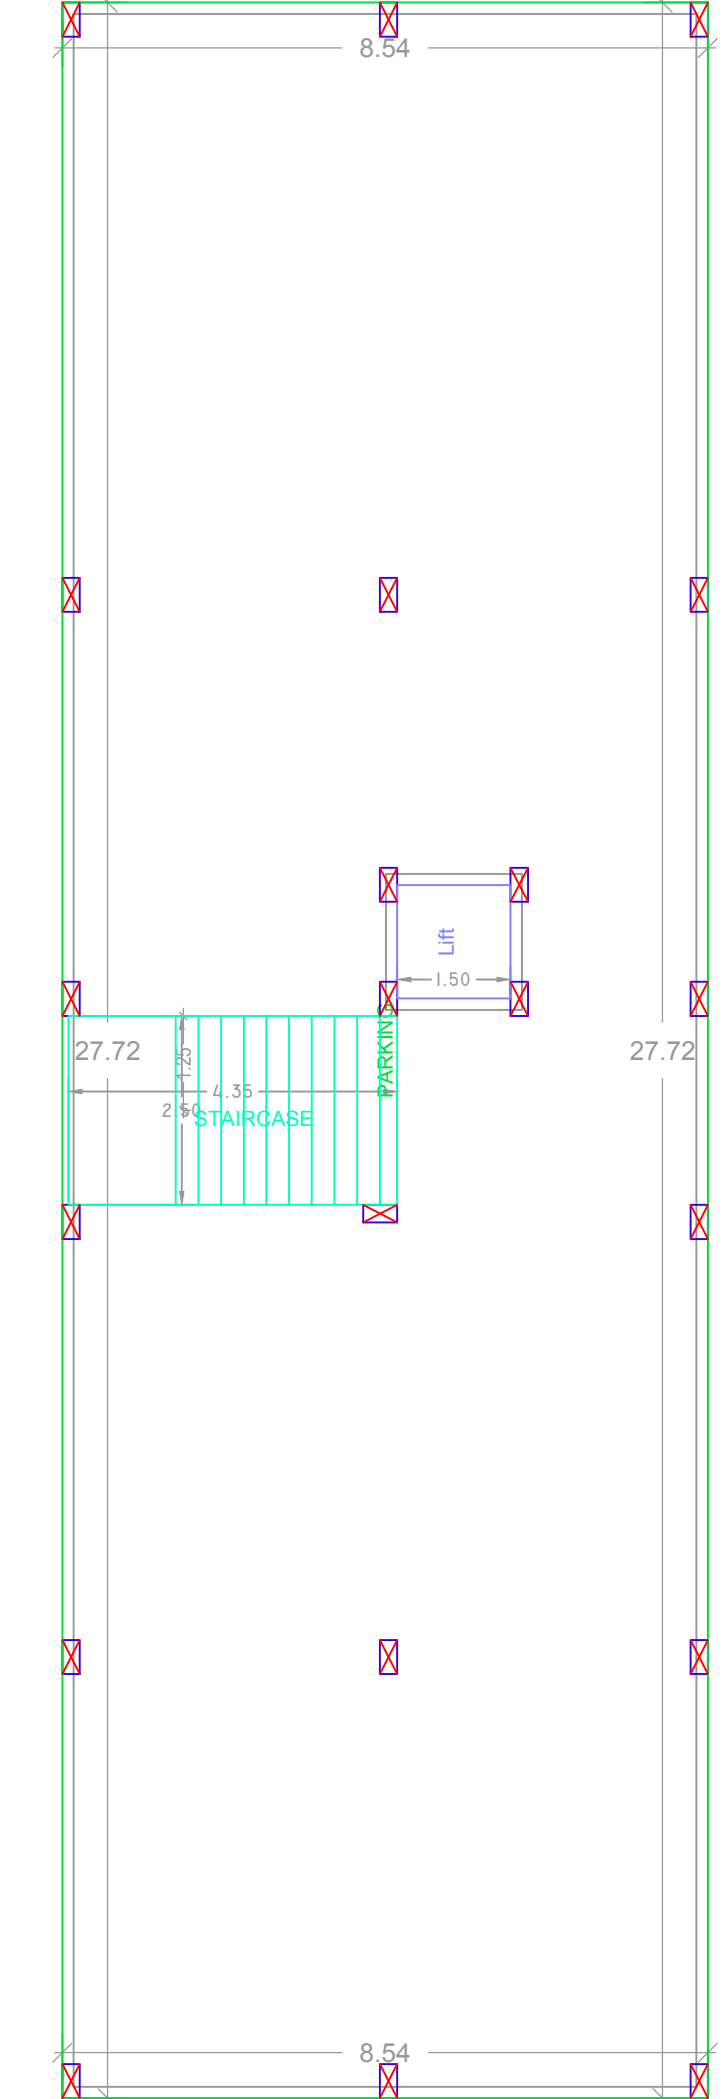

BUILDING USE/SUBUSE DETAILS	
BUILDING NAME	MPL (RUBRICON INFRA)
BUILDING USE	Residential
BUILDING SUBUSE	Residential Apartment
BUILDING TYPE	NA
FLOOR DETAILS	1 Stilt + 5 upper floors

NET BUILT UP AREA AND DWELLING UNITS DETAILS				
BUILDING NAME	NO OF BLDG	TOTAL BUA	NET BUA	THMTS.
MPL (RUBRICON INFRA)	1	1422.60	1183.65	10
GRAND TOTAL	1	1422.60	1183.65	10.00

COLOR INDEX				
PLT BOUNDARY	ABUTTING ROAD	PROPOSED CONSTRUCTION	COMMON PLOT	ROAD WIDENING AREA
EXISTING (To be retained)	EXISTING (To be retained)	EXISTING (To be retained)	EXISTING (To be retained)	EXISTING (To be retained)

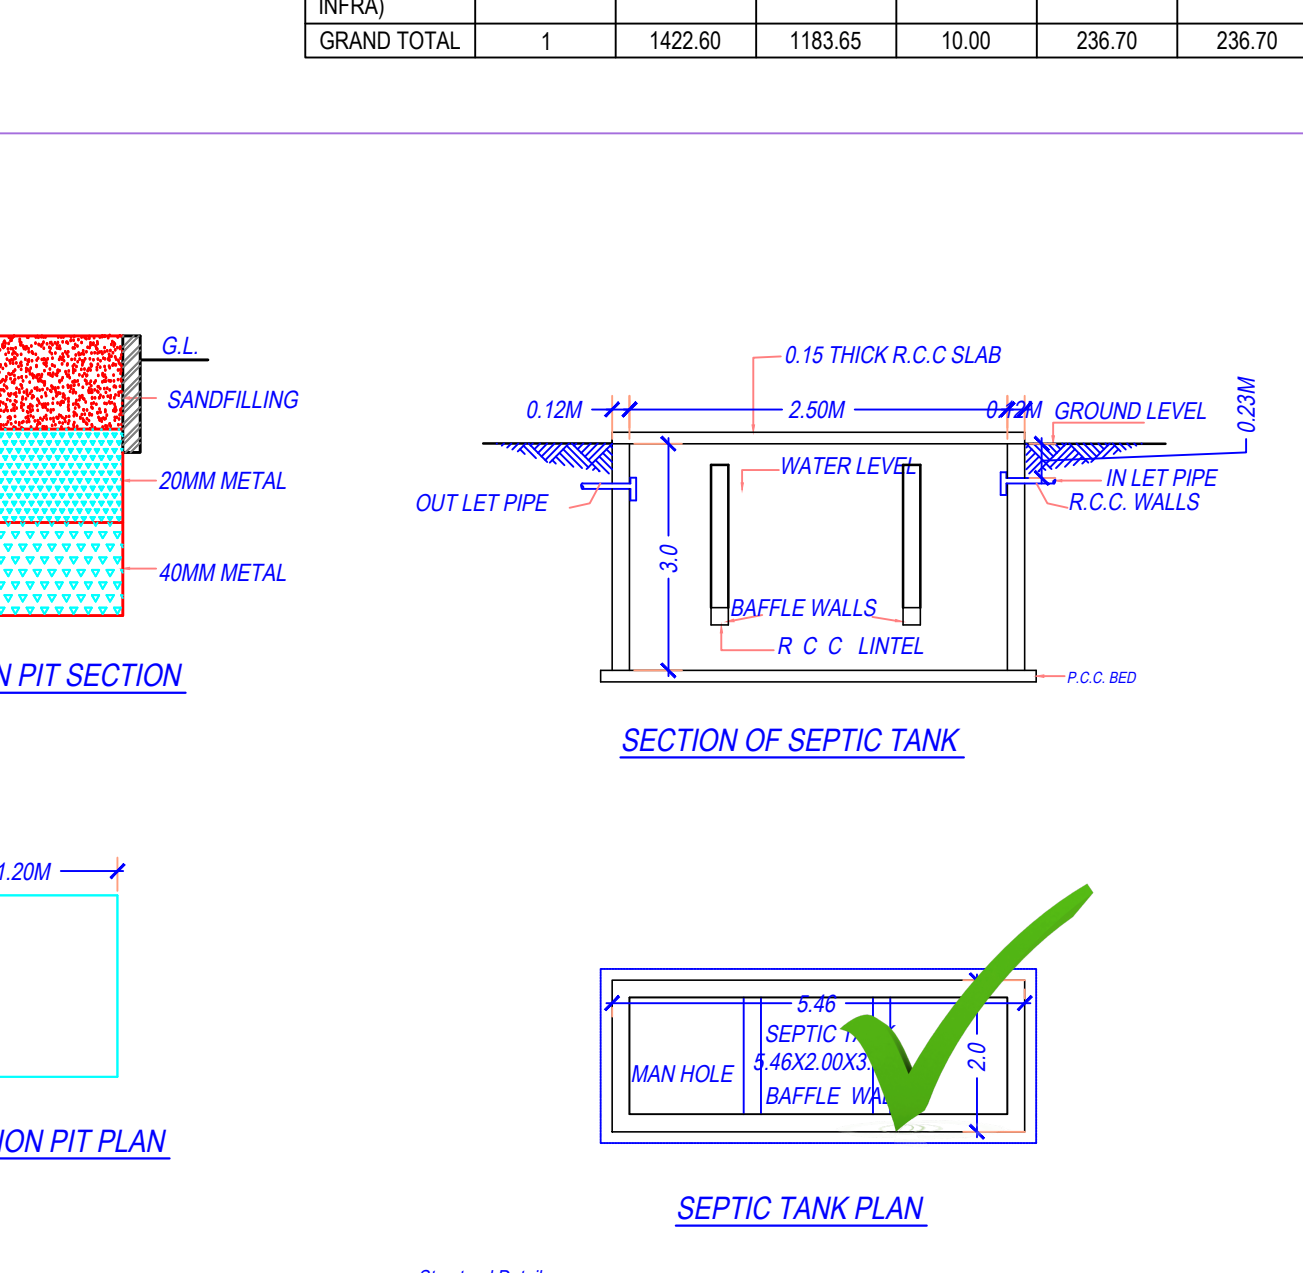

OWNERS NAME AND SIGNATURE
BUILDERS NAME AND SIGNATURE
ARCHITECTS NAME AND SIGNATURE
STRUCTURAL ENGINEERS NAME AND SIGNATURE
SEAL OF APPROVAL

Note: All dimensions are in meters.