


EXISTING 12m WIDE ROAD

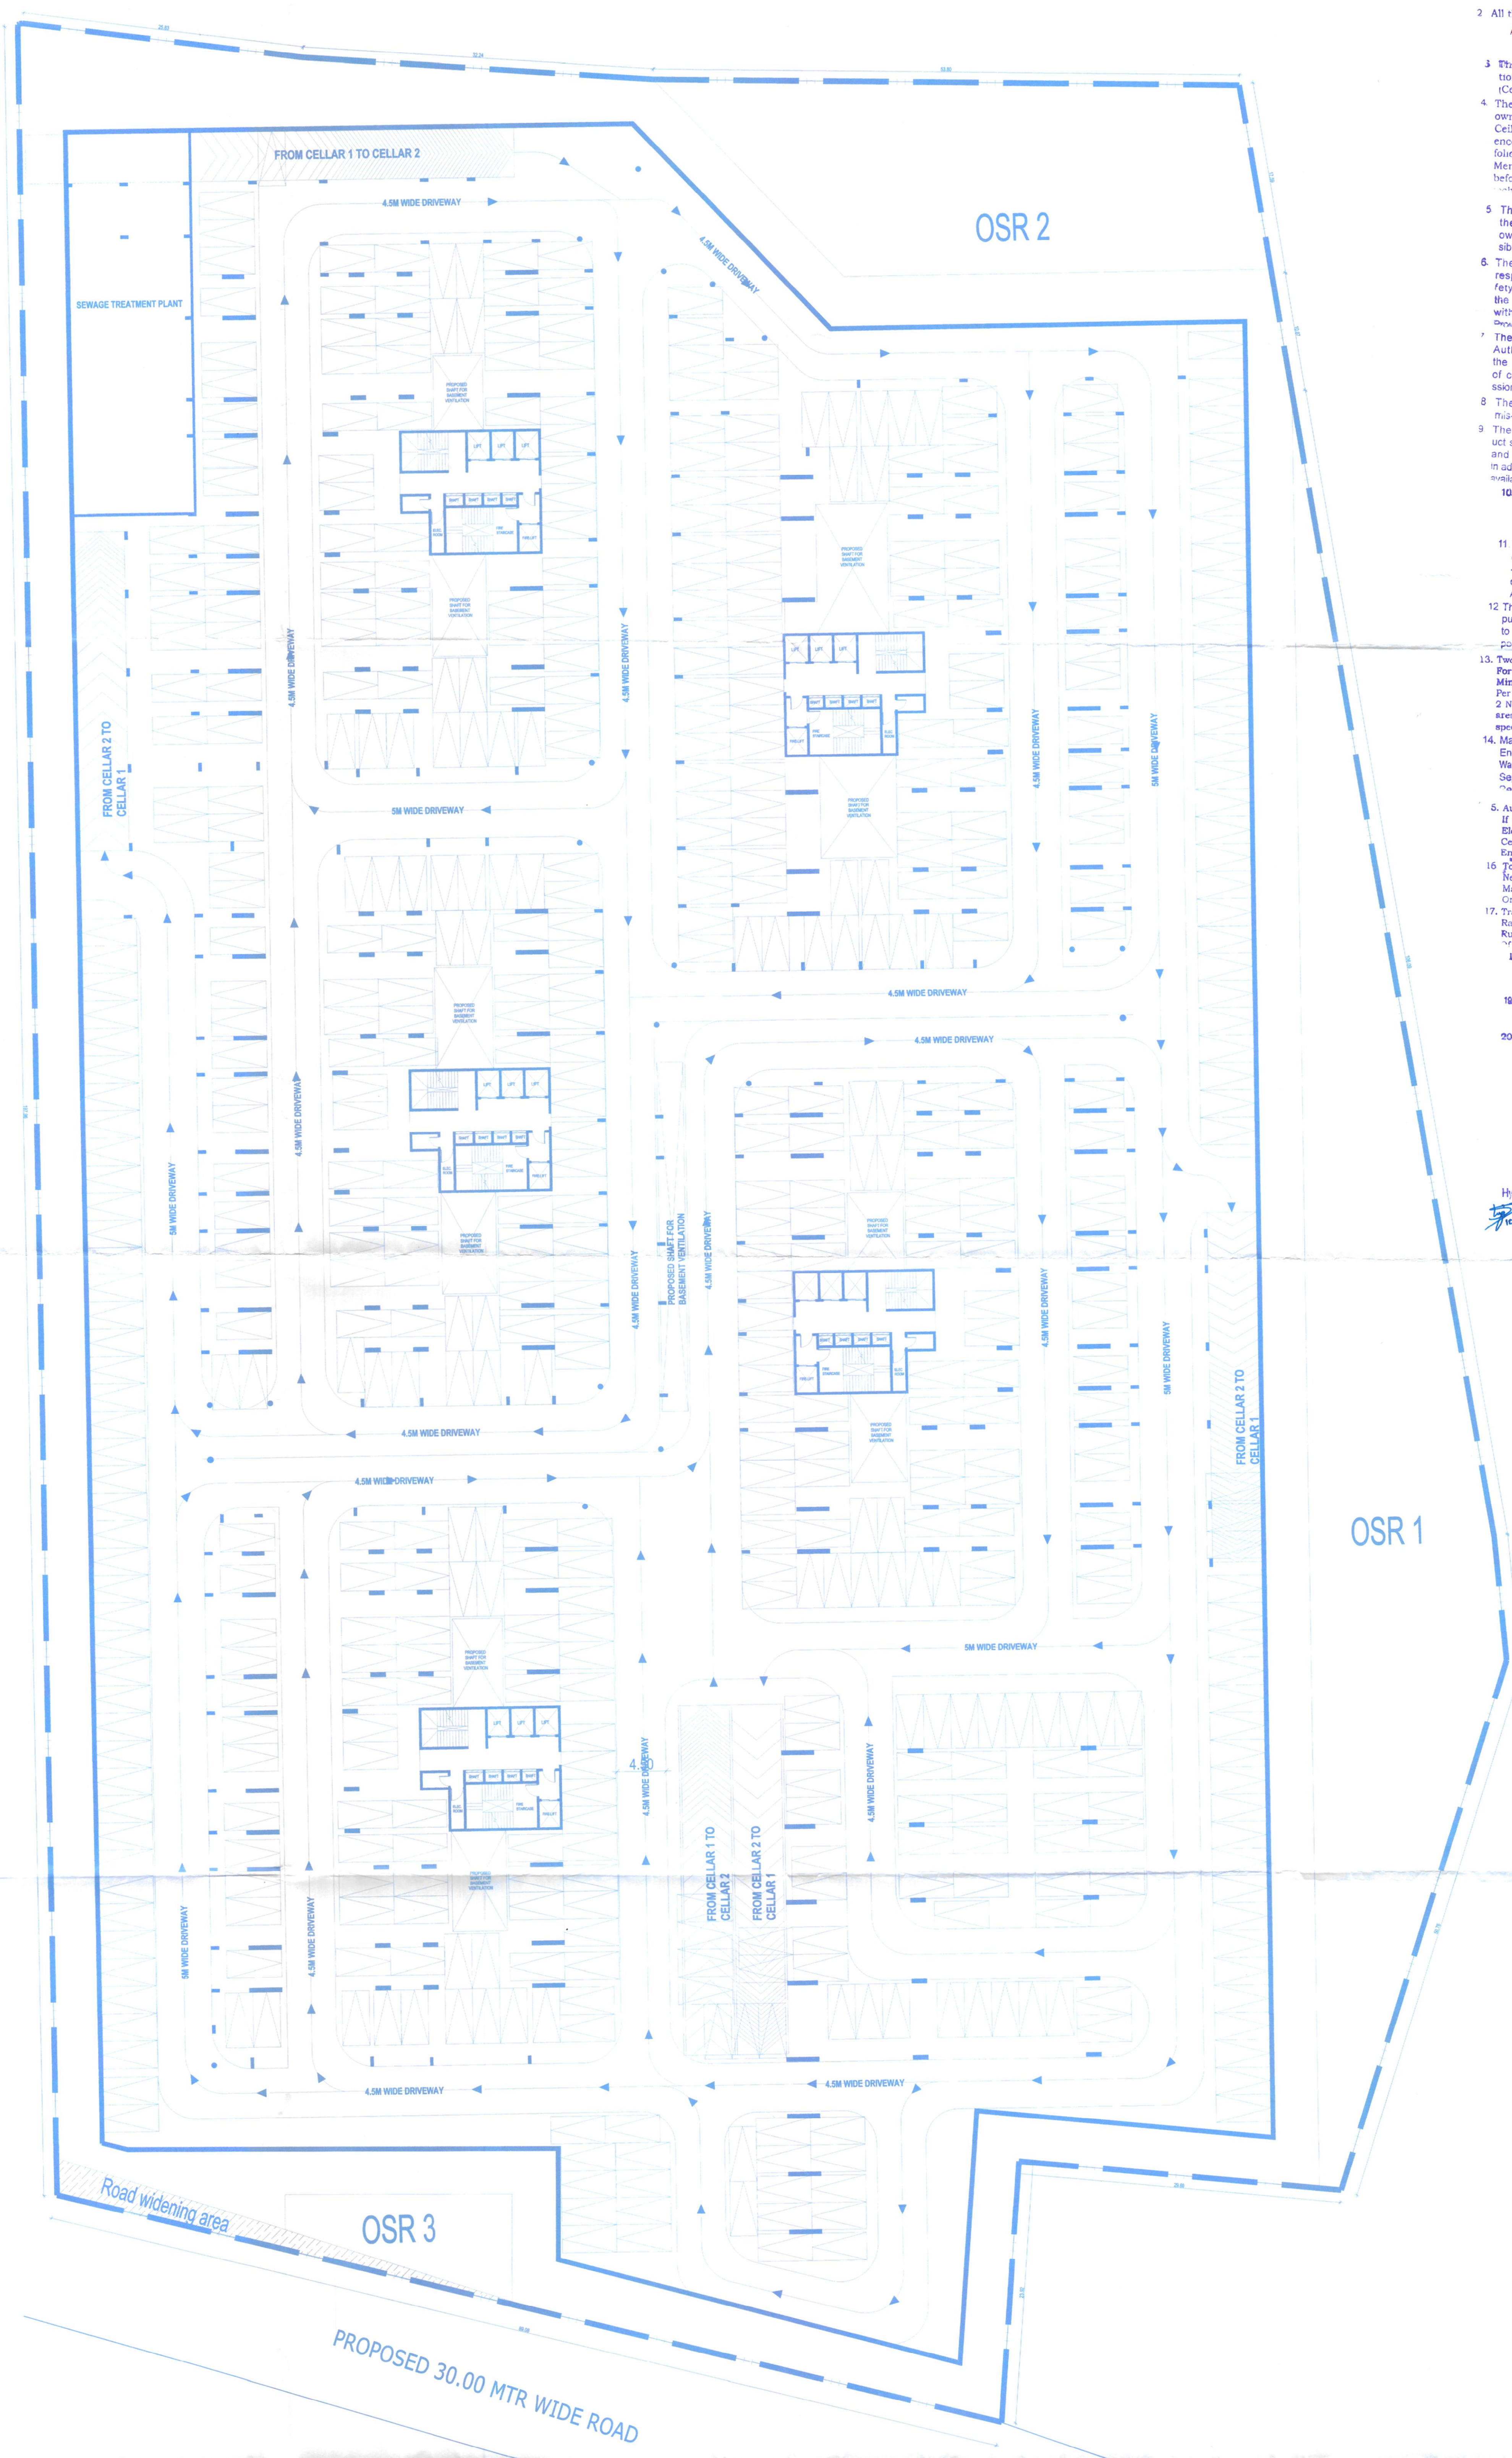

1. ALL WORKS TO BE ACCORDED ONLY FOR DWELLING UNITS UNDER SECTION 20(2) I, II OF HYDERABAD METROPOLITAN DEVELOPMENT AUTHORITY ACT 2006 & FORWARDED TO THE MUNICIPALITY LOCAL BODY FOR FINAL SANCTION SUBJECT TO CONDITIONS MENTIONED ON APPROVED PLAN.
2. All the conditions mentioned in the plan shall be strictly followed.
3. This approval does not bar the application of the provision of the Urban Land (Ceiling & Regulation) Act, 1976.
4. The local authority shall ensure that ownership clearance (and Urban Land Ceiling) clearance of the site under reference are in order and should scrupulously follow the Government instructions vide Memo No. 1933/1/11/97 MA, dt 18-6-07 before sanctioning and releasing the technical approved building plans.
5. This approval does not confer or assign the ownership of the site boundary is the responsibility of the applicant.
6. The Builder/Developer/Owner shall be responsible and ensure the fire safety structural stability requirements of the proposed complex are in accordance with the National Building Code, 2016.
7. The Commissioner of Municipality/Local Authority should physically take over the land shown in Road widening at time of cost before releasing Building permission as per statutory Master Plan 2012.
8. The Cellar/Slit parking should not be misused for any other purpose.
9. The Builder/Developer should construct sump, drainage as per ISI Standards and to the satisfaction of Municipality in addition to the drainage system available.
10. THAT THE APPLICANT SHALL COMPLY THE CONDITIONS LAD DOWN G.O.M.S. NO. 470 M.A. Dt. 8-7-2006, G.O.M.S. NO. 168 M.A. Dt. 7-4-2012 AND ITS ENDORSEMENTS.
11. The applicant shall obtain necessary clearance from the FIRE SERVICES DEPARTMENT for the proposed Apartment complex/Building as per the provision of A.P. FIRE SERVICES ACT, 1999.
12. This permission does not give any public agency include HMDA/Local Body to acquire the lands for public purpose as per Law.
13. Two numbers water type fire extinguisher For every 600 Sq. Mtrs of floor area with Minimum of four numbers fire extinguisher For food and 5 Nos. DCP extinguisher minimum 2 Nos. each at Generator and Transformer area shall be provided as per Bureau of Fire specification No.2190-1992.
14. Manually operated and alarm system in the Entire Building: Separate Underground static Water storage tank capacity of 25,000 lts capacity. Separate Terrace tank of 25,000 lts Capacity for Residential Buildings, House Rool Down Corn
15. Automatic Sprinkler system is to be provided if the basement area exceeds 200 Sq. Mtrs. Electrical wiring and installation shall be Certified by the electrical engineers to ensure electrical fire safety.
16. To create a joint open space with the Neighbourhood building / premises for Maneuverability of fire vehicles. No parking Group constructions shall be made in this area.
17. Transformers shall be provided with 4 hours Rating fire resistant constructions as per Rule, Fire of A.P. Apartment (Prevention of) construction and ownership rules.
18. To provide one entry and one exit To the premises with a minimum Width of 4.5 mtrs and height Clearance of 5 mtrs.
19. To provide sewage treatment plant or septic Or sewage water for usage of recycled water for Gardening etc. as per APDCB Norms.
20. Provide Fire resistant rating 0001 For the collapsible life in all floors Provide Generator, as alternate Source of electric supply, Emergency Lighting in the corridors/ common Passages and stair cases.

For METROPOLITAN COMMISSIONER
Hyderabad Metropolitan Development Authority

TITLE	SHEET NO. 3, TOTAL No. OF SHEETS - 6
PLAN SHOWING THE PROPOSED CONSTRUCTION OF RESEDENTIAL APARTMENT IN SY.NO.121/PART, SITUATED AT TATIANNARAM VILLAGE, ABDULAPURMET MANDAL (PREVIOUSLY KNOWN AS HAYATHNAGAR MANDAL, RANGA REDDY DISTRICT.	
BELONGING TO:	
SRI C. AMARENDER REDDY & OTHERS REPRESENTED BY THEIR GPO HOLDER "NAMISHREE PROJECTS" REPRESENTED BY SRI. MOTILAL JAIN	
SCHEDULE OF OPENINGS	
MAIN DOOR (MD)	: 1.07M X 2.4M
SINGLE FLUSH DOOR (D1)	: 0.90M X 2.1M
SINGLE FLUSH DOOR (D2)	: 0.75M X 2.1M
SINGLE FLUSH DOOR (D3)	: 1.10M X 2.1M
SLIDING DOOR (SD1)	: 2.40M X 2.4M
SLIDING DOOR (SD2)	: 1.20M X 2.4M
FIRE DOOR (FRD)	: 1.20M X 2.4M
SLIDING WINDOW (W1)	: 1.80M X 1.50M
SLIDING WINDOW (W2)	: 1.20M X 1.50M
SLIDING WINDOW (W3)	: 0.75M X 1.20M
SLIDING WINDOW (KW)	: 1.20M X 1.50M
VENTILATOR (V)	: 0.60M X 1.20M
AREA STATEMENT	
TOTAL LAND AREA : 6.15 ACRES (OR) 29789.18 SYD (OR) 24907.34 SMT	
ROAD WIDENING AREA : 95.97 SYD (OR) 80.24 SMT	
NET LAND AREA : 29693.21 SYD (OR) 24827.10 SMT	
BLOCK A	
GROUND FLOOR : 128.42 SMT	
TYPICAL FLOOR AREA : 955.02 SMT x 24 = 22,920.48 SMT	
NINETEENTH FLOOR AREA : 1004.81 SMT	
TOTAL BUILT-UP AREA : 24,053.71 SMT	
BLOCK B	
GROUND FLOOR : 128.42 SMT	
TYPICAL FLOOR AREA : 955.02 SMT x 24 = 22,920.48 SMT	
NINETEENTH FLOOR AREA : 1004.81 SMT	
TOTAL BUILT-UP AREA : 24,053.71 SMT	
BLOCK C	
GROUND FLOOR : 128.42 SMT	
TYPICAL FLOOR AREA : 955.02 SMT x 24 = 22,920.48 SMT	
NINETEENTH FLOOR AREA : 1004.81 SMT	
TOTAL BUILT-UP AREA : 24,053.71 SMT	
BLOCK D	
GROUND FLOOR : 128.42 SMT	
TYPICAL FLOOR AREA : 955.02 SMT x 24 = 22,920.48 SMT	
NINETEENTH FLOOR AREA : 1005.29 SMT	
TOTAL BUILT-UP AREA : 24,054.19 SMT	
BLOCK E	
GROUND FLOOR : 128.42 SMT	
TYPICAL FLOOR AREA : 955.02 SMT x 24 = 22,920.48 SMT	
NINETEENTH FLOOR AREA : 1005.29 SMT	
TOTAL BUILT-UP AREA : 24,054.19 SMT	
TOTAL AREA (BLOCKS A, B, C, D & E) : 1,20,269.51 SMT	
AMENITIES BLOCK AREA REQUIRED 3% OF 1,20,269.51 : 3608.08 SMT	
AMENITIES BLOCK AREA PROVIDED : 6085.01 SMT	
PARKING AREA REQUIRED (RESIDENTIAL) : 22% = 28467.27 SMT	
PARKING AREA PROVIDED : 37236.70 SMT	
CELLAR FLOOR AREA : 18733.60 SMT	
SUB CELLAR FLOOR AREA : 18503.10 SMT	
VENTILATION REQUIRED 2.5% OF CELLAR AREA : 490.71 SMT	
VENTILATION PROVIDED OF CELLAR AREA : 547.04 SMT	
TOT-LOT REQUIRED 10% OF NET LAND AREA : 2484.874 SMT	
TOT-LOT PROVIDED : 2527.07 SMT	
TOTAL NO OF UNITS: 625, LARGE UNITS=500, SMALL UNITS=125	
TOTAL NO OF CARS:	
BASEMENT-1=496 NOS	
BASEMENT-2=496 NOS	
SURFACE PARKING=119 NOS	
TOTAL NO OF CARS (PROVIDED) = 1111 NOS	
10% MORTGAGE AREA REQUIRED : 12635.42 SMT	
5% MORTGAGE AREA REQUIRED : 6317.71 SMT	
TOTAL MORTGAGE AREA REQUIRED : 18953.13 SMT	
TOTAL MORTGAGE AREA PROVIDED : 19294.50 SMT	
TOTAL NO OF FLOORS	
BLOCK A,B,C,D&E - SUB CELLAR+CELLAR+GROUND+25 FLOORS	
OWNER'S SIGN	
Builder's Sign	
STRUCTURAL CONSULTANT	
ARCHITECT	
Scale : As indicated	
Date : 18/07/2023	
CELLAR FLOORPLAN - 2	