

AMINITIES FLOOR PLANS

TITLE SHEET NO. 6 TOTAL No. OF SHEETS : 6

PLAN SHOWING THE PROPOSED CONSTRUCTION OF RESEIDENTIAL APARTMENT IN SY.NO.121/PART, SITUATED AT TATIANARAM VILLAGE, ABDULAPURMET MANDAL (PREVIOUSLY KNOWN AS HAYATHNAGAR MANDAL, RANGA REDDY DISTRICT.

BELONGING TO:

SRI C. AMARENDER REDDY & OTHERS REPRESENTED BY THEIR GPO HOLDER "NAMISHREE PROJECTS" REPRESENTED BY SRI. MOTILAL JAIN

SCHEDULE OF OPENINGS


MAIN DOOR (MD)	: 1.07M X 2.4M
SINGLE FLUSH DOOR (D1)	: 0.90M X 2.1M
SINGLE FLUSH DOOR (D2)	: 0.75M X 2.1M
SINGLE FLUSH DOOR (D3)	: 1.10M X 2.1M
SLIDING DOOR (SD1)	: 2.40M X 2.4M
SLIDING DOOR (SD2)	: 1.20M X 2.4M
FIRE DOOR (FRD)	: 1.20M X 2.4M
SLIDING WINDOW (W1)	: 1.80M X 1.50M
SLIDING WINDOW (W2)	: 1.20M X 1.50M
SLIDING WINDOW (W3)	: 0.75M X 1.20M
SLIDING WINDOW (W4)	: 1.20M X 1.50M
VENTILATOR (V)	: 0.60M X 1.20M

AREA STATEMENT

CLUBHOUSE

GROUND FLOOR	: 1125.21 SMT
FIRST FLOOR	: 962.11 SMT
SECOND FLOOR	: 689.47 SMT
THIRD FLOOR	: 1142.93 SMT
FOURTH FLOOR	: 1142.93 SMT
FIFTH FLOOR	: 1022.35 SMT


TOTAL BUILT-UP AREA : 6085.01 SMT

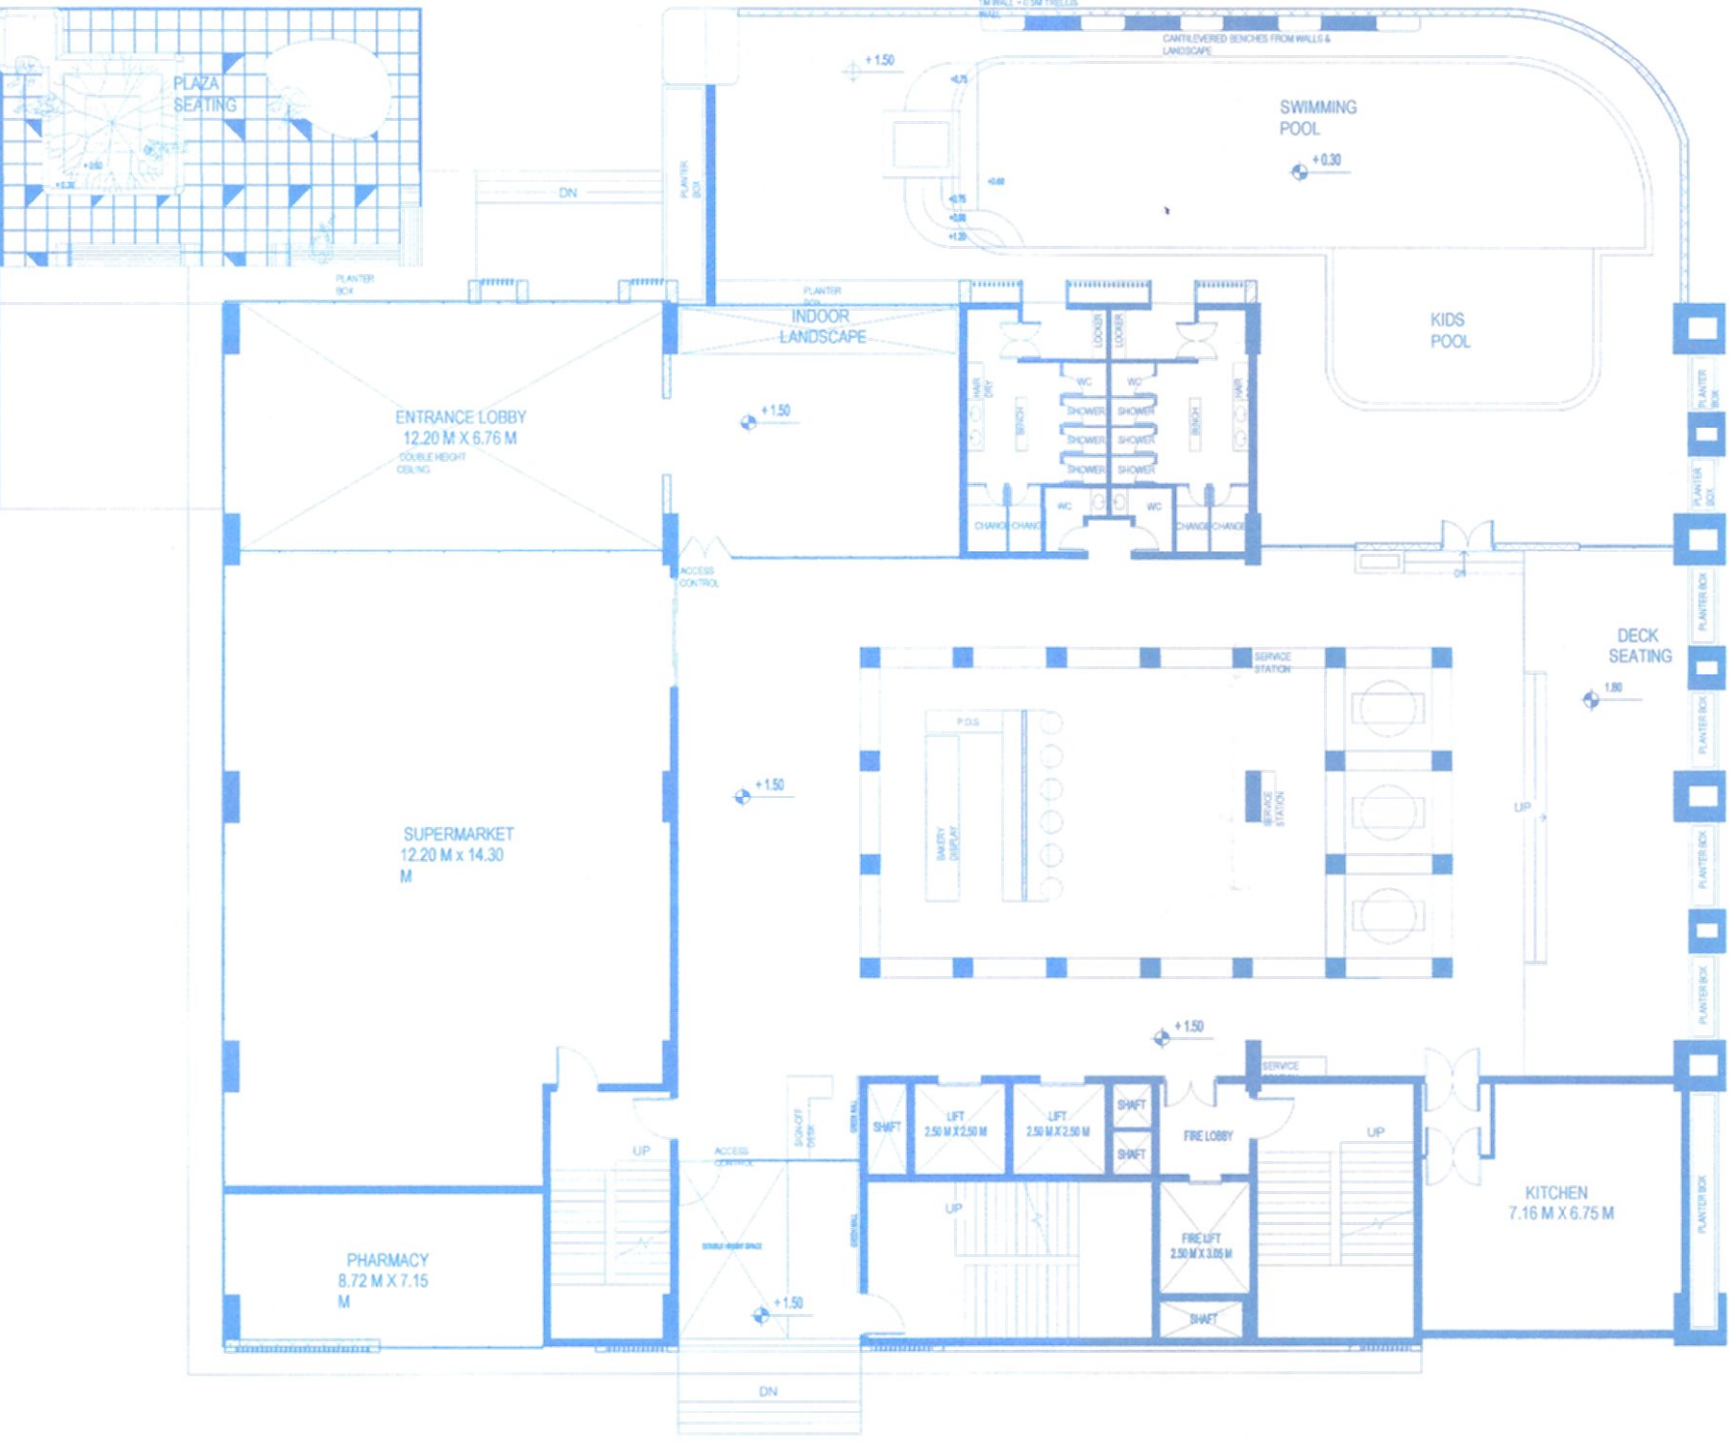


GROUND FLOORPLAN




THIRD FLOORPLAN

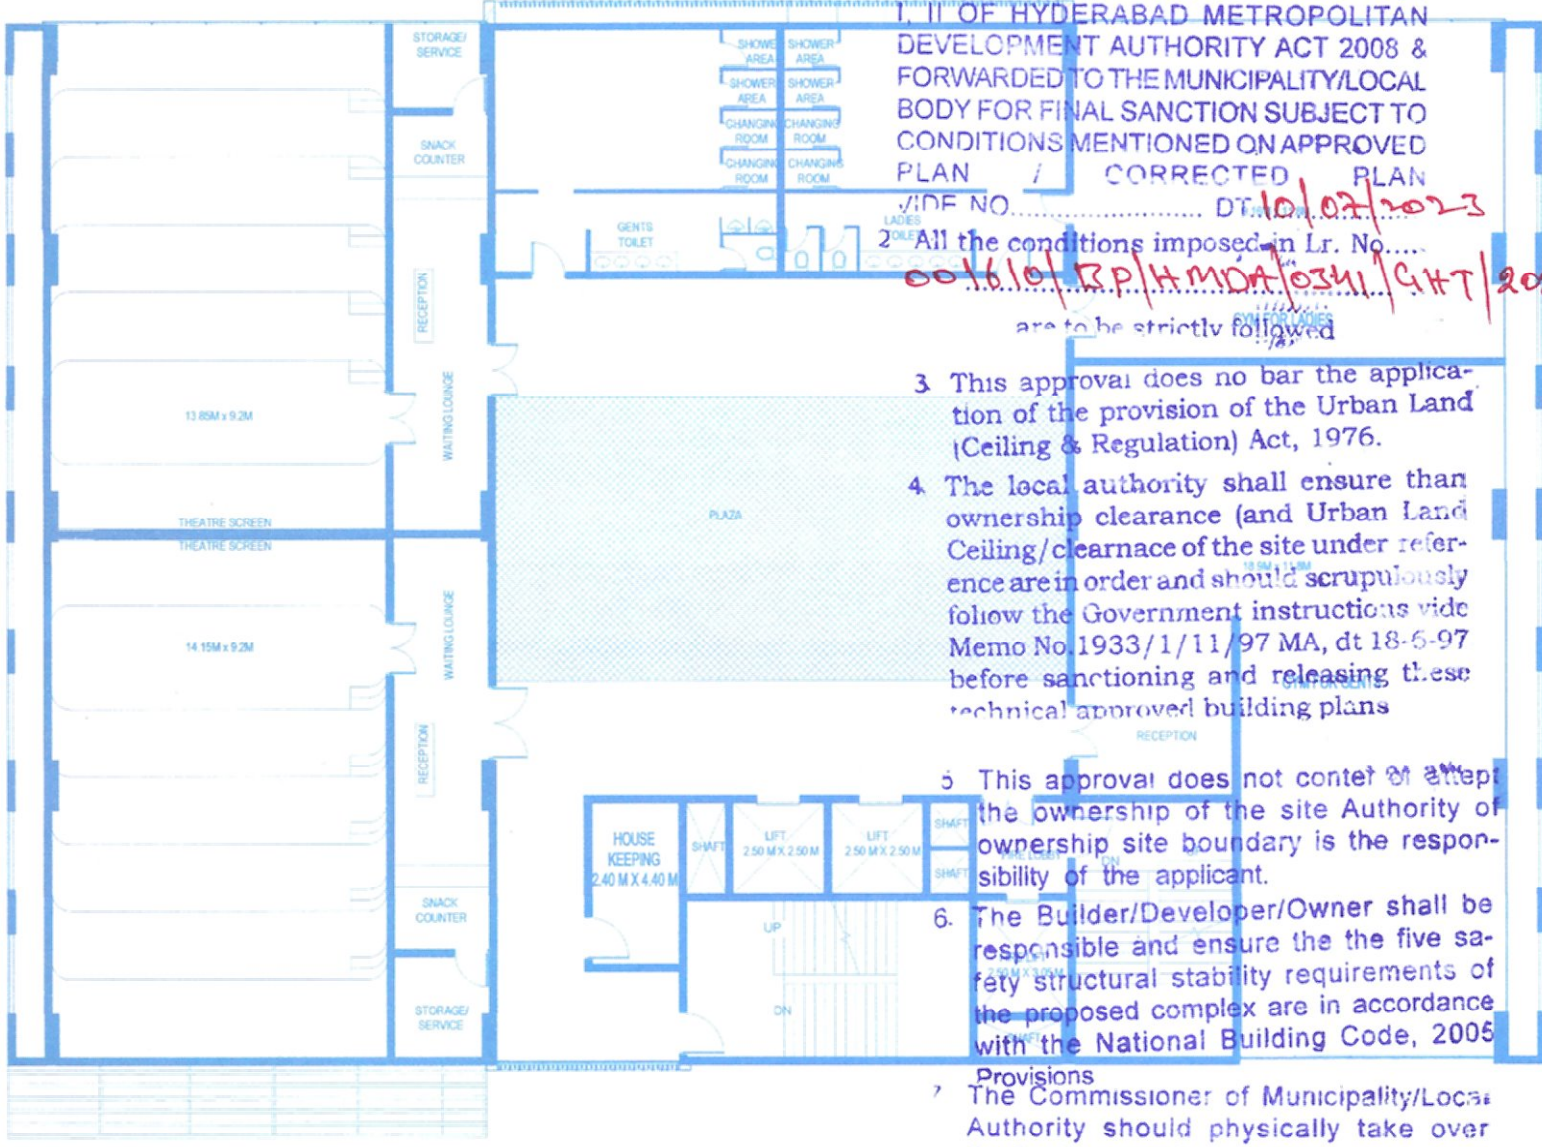

FOURTH FLOORPLAN

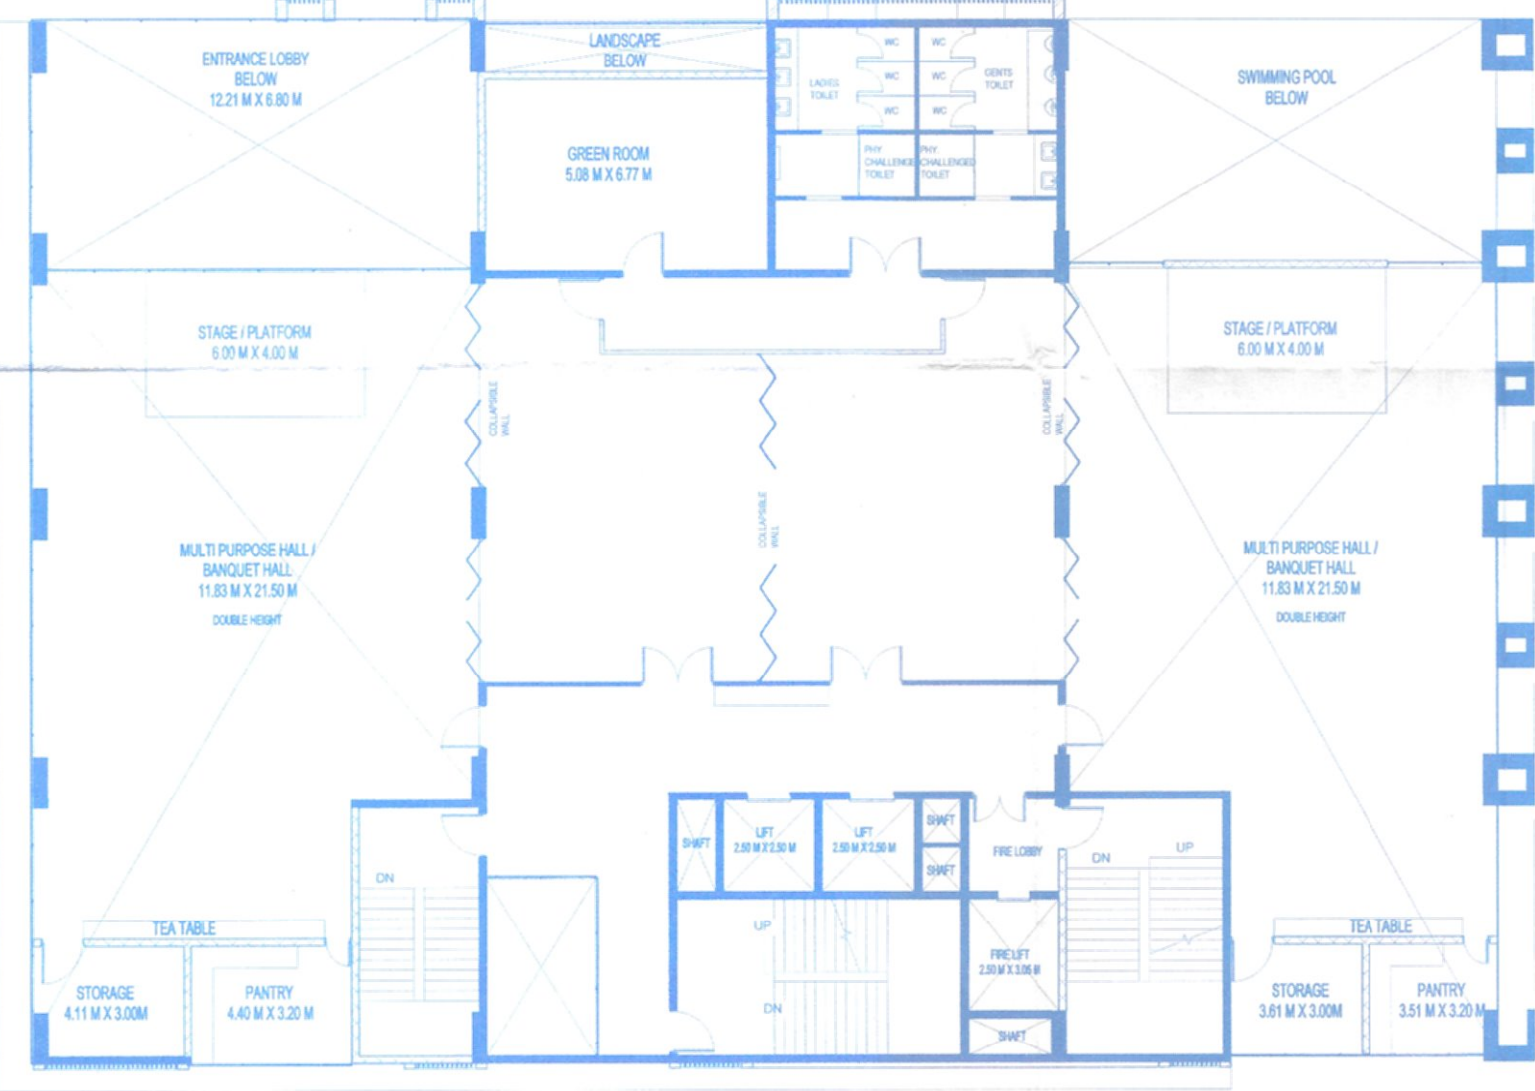


FIRST FLOORPLAN

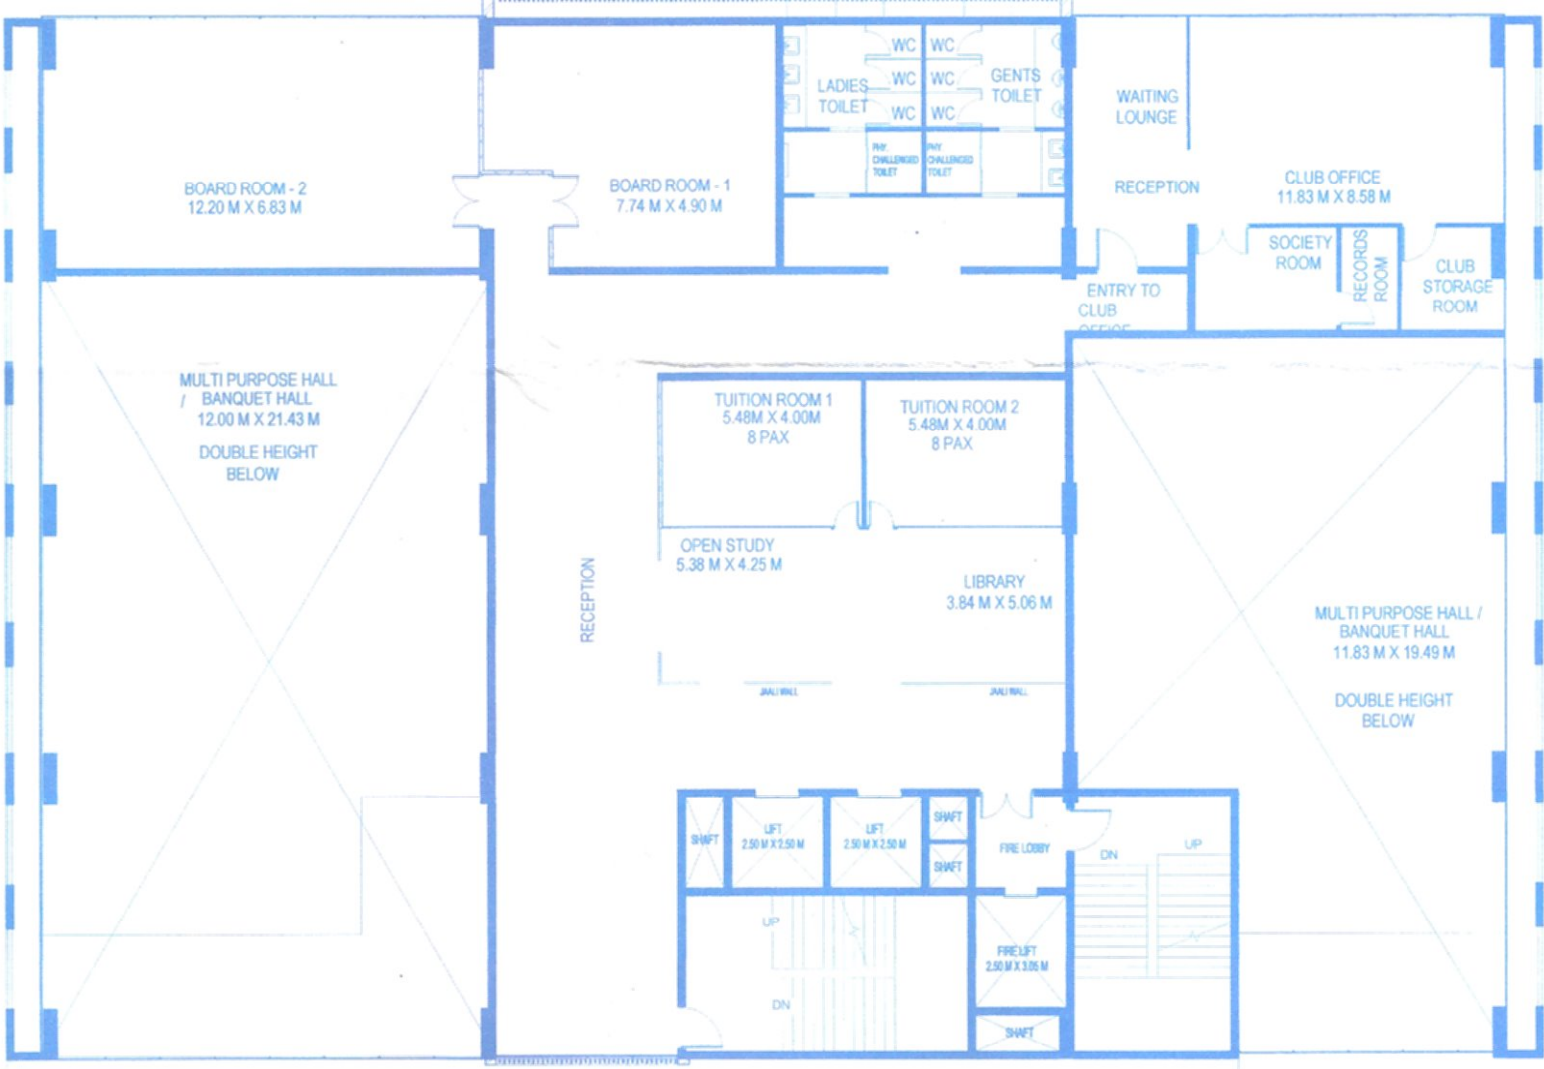


SECOND FLOORPLAN



FIFTH FLOORPLAN

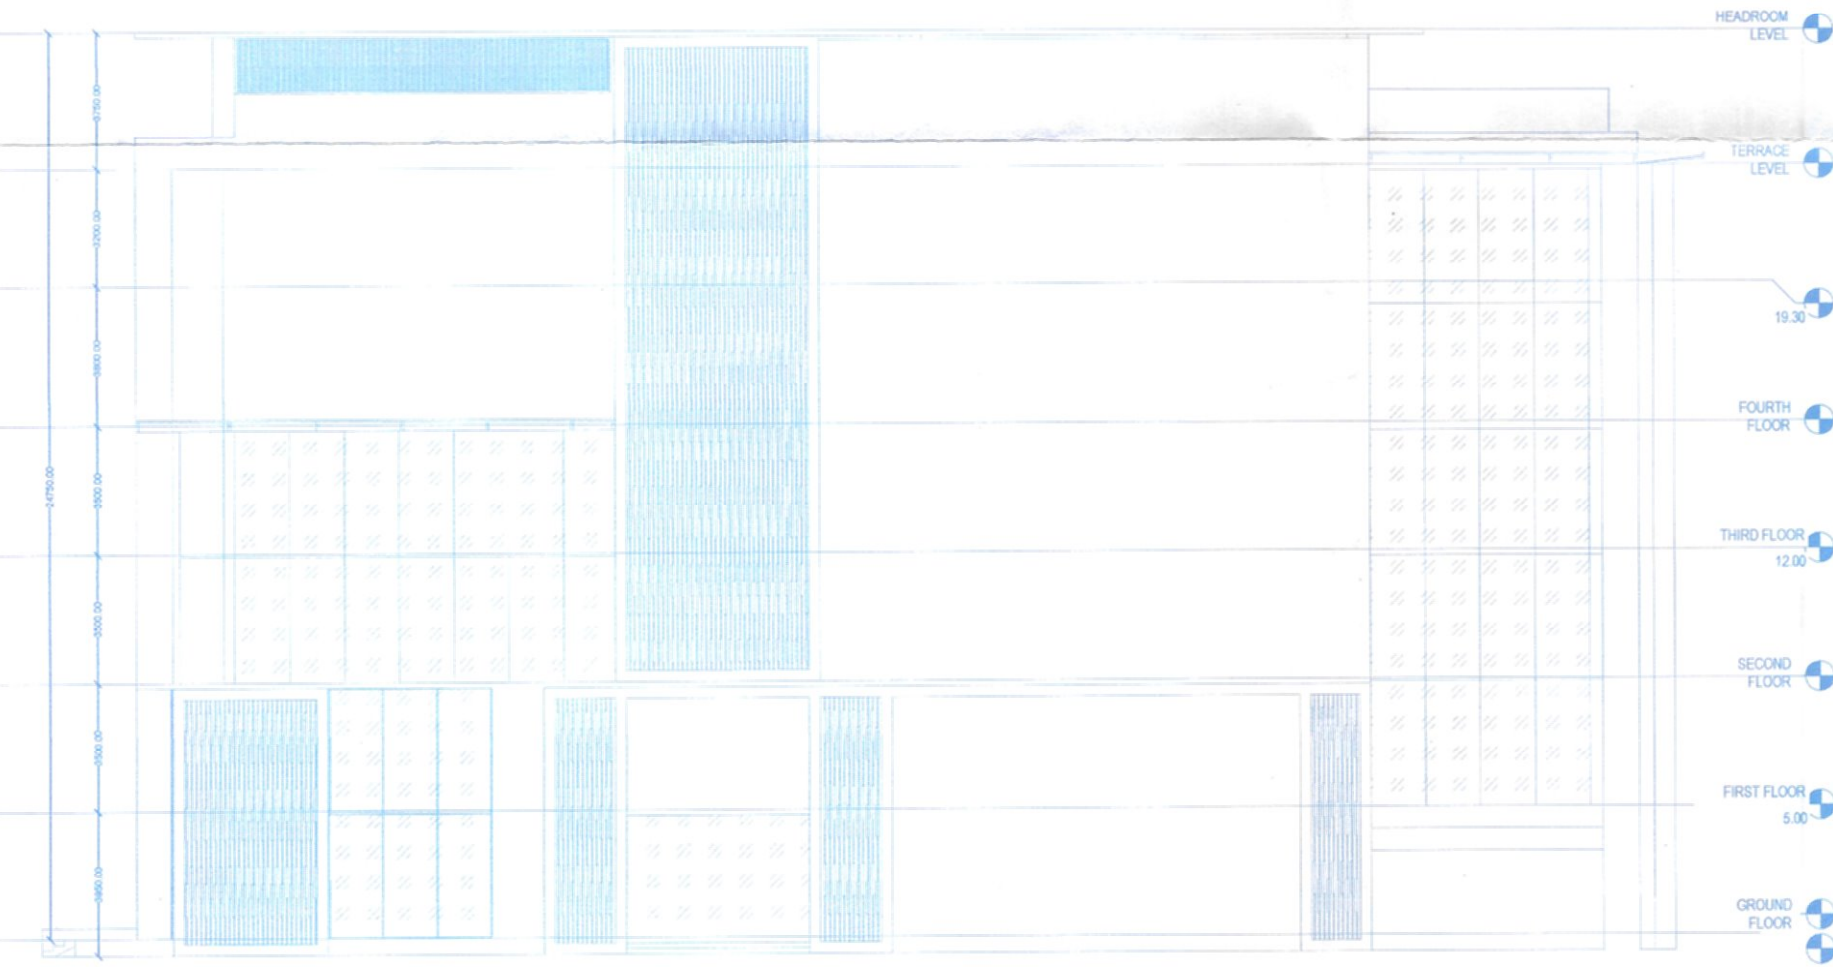

SOUTH ELEVATION

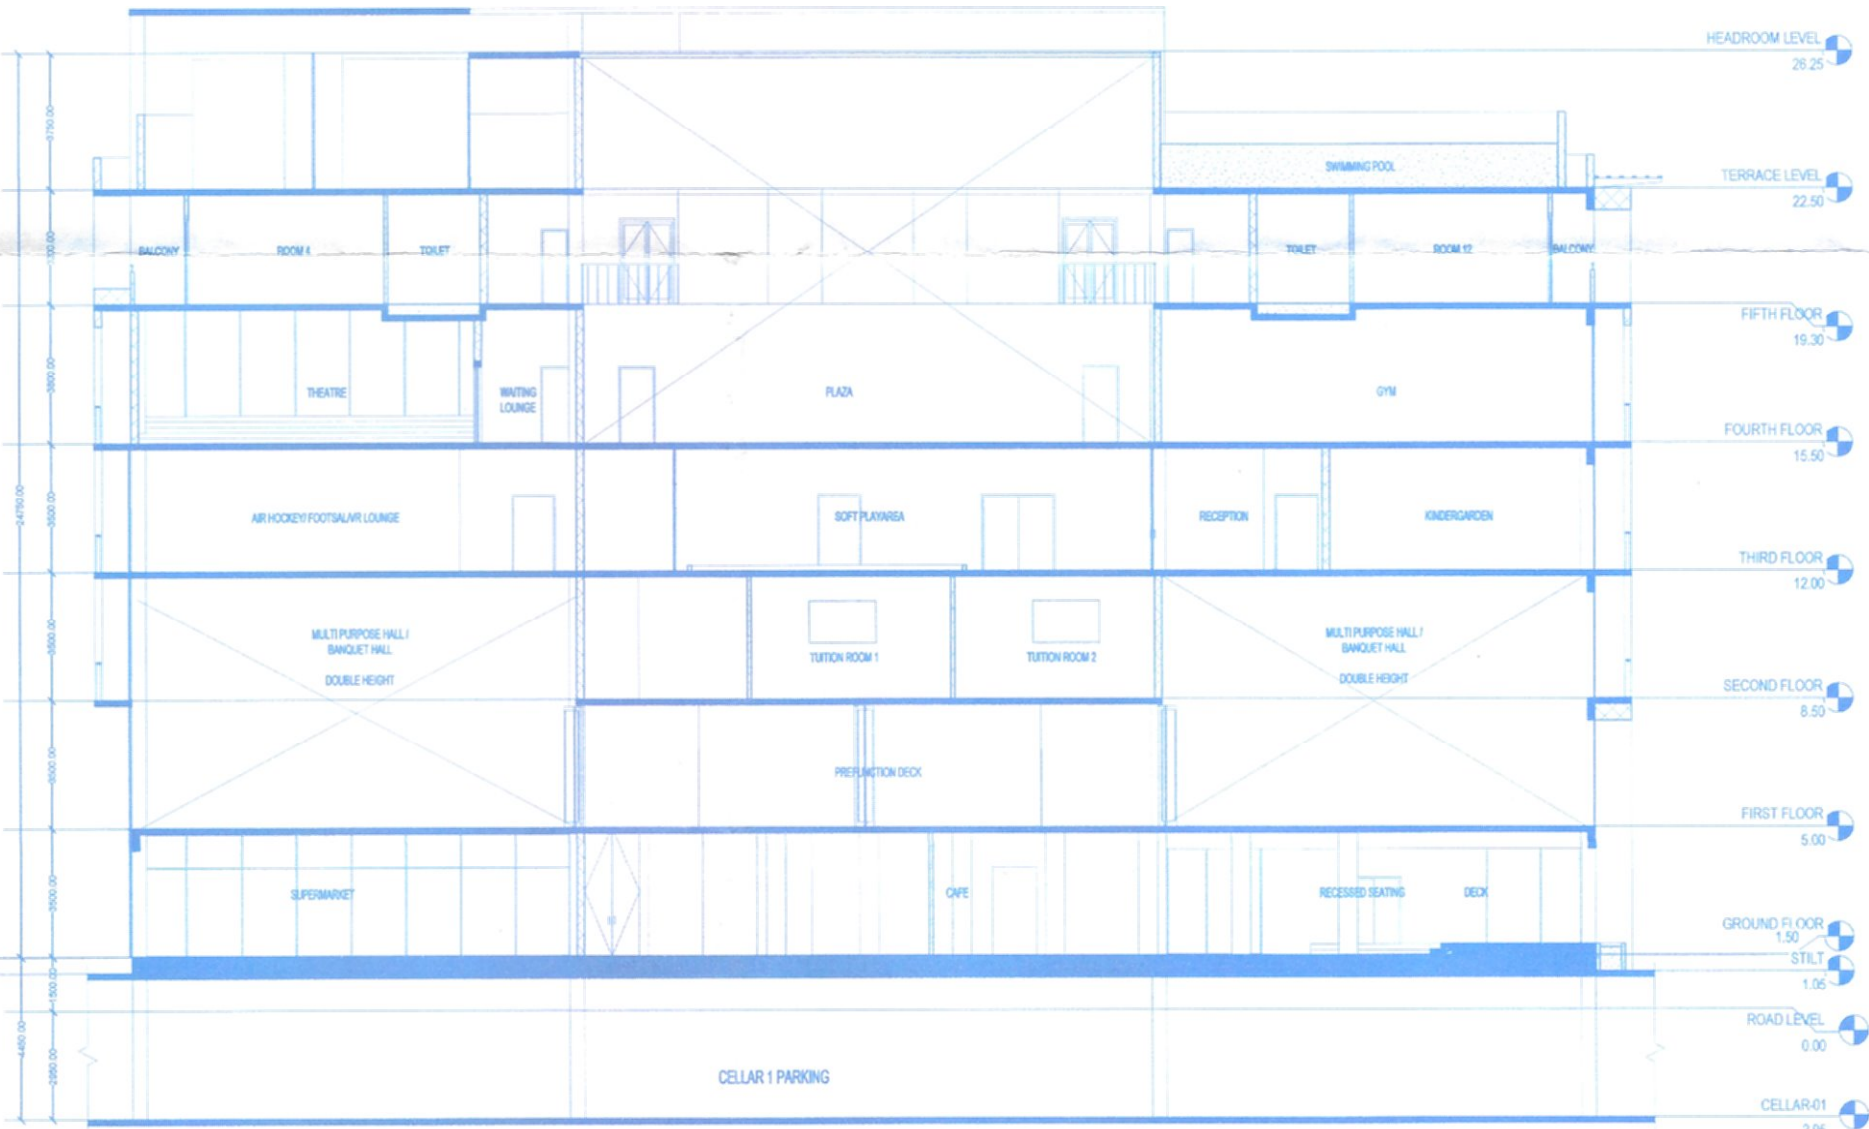

SECTION-CC'



TERRACE FLOORPLAN

TECHNIC APPROVAL IS HERE BY ACCORDED ONLY FOR DWELLING UNITS UNDER SECTION 20(2) OF HYDERABAD METROPOLITAN DEVELOPMENT ACT 2008 & FORWARDED TO MUNICIPALITY/LOCAL BODY FOR FINAL SANCTION SUBJECT TO CONDITIONS MENTIONED ON APPROVED PLAN CORRECTED PLAN DATE NO. 01.10.2023 001101 R.P.H.M.D.A./341/947/2023.

2. All the conditions imposed in Lr. No. 001101 R.P.H.M.D.A./341/947/2023 are to be strictly followed.

3. This approval does not bar the application of the provision of the Urban Land (Ceiling & Regulation) Act, 1976.

4. The local authority shall ensure that ownership clearance (and Urban Land Ceiling/clearance of the site under reference are in order and shall scrupulously follow the Government instructions vide Memo No.1933/1/11/97 MA, dt.18-6-97 before sanctioning and releasing these technical approved building plans.

5. This approval does not confer or accept the ownership of the site Authority of ownership site boundary is the responsibility of the applicant.

6. The Builder/Developer/Owner shall be responsible and ensure that the five safety structural stability requirements of the proposed complex are in accordance with the National Building Code, 2005 Provisions.

7. The Commissioner of Municipality/Local Authority should physically take over the land shown in Road widening at free of cost before releasing Building permission as per statutory Master Plan Z D F.

8. The Cellar/shed parking should not be mis-used for any other purpose.

9. The Builder/Developer should construct sump, drainage as per ISI Standards and to the satisfaction of Municipality in addition to the drainage system available.

10. THAT THE APPLICANT SHALL COMPLY THE CONDITIONS Laid Down G.O.M.S. NO: 470 M.A. Dt: 3-3-1998 G.O.M.S. NO: 168 M.A. Dt: 2-4-2015 AND ITS ENDOWMENTS.

11. The applicant shall obtain necessary clearance from the FIRE SERVICES DEPARTMENT for the proposed Apartment complex/Building as per the provisions of A.P. FIRE SERVICES ACT, 1999.

12. This permission does not entitle any public agency including the Local Body to acquire the lands for public purpose as per Law.

13. Two numbers water type fire extinguishers for every 600 Sq.Mtrs of floor area with Minimum of four numbers fire extinguisher per floor and 5 Nos. DCP extinguisher minimum 2 Nos. each at generator and transformer area shall be provided as per IS: 15001 specifically in No. 1, 190-1, 1922.

14. Manually operated and alarm system in the Entire Building. Separate Underground static Water storage tank capacity of 25,000 Ltrs. capacity Separate Terrace tank of 35,000 Ltrs. capacity for Residential Buildings. House Rati Down Com.

15. Automatic Sprinkler system is to be provided if the basement area exceeds 200 Sq. mtrs. Electrical wiring and installation shall be Certified by the electrical engineers to ensure electrical fire safety.

16. There shall be a joint open space with the Neighbouring building / premises for the Maneuverability of fire vehicles. No parking Orany constructions shall be made in setbacks area.

17. Transformers shall be provided with 4 hours Rating fire resistant constructions as per Rule 15(e) of A.P. Apartments (Promotion of construction and ownership) rules 1987.

18. To provide one entry and on exit To the premises with a minimum Width of 4.5 mtrs and height Clearance of 5 mtrs.

19. To provide sewerage treatment plant for recycling Of sewage water for usage of recycled water for Gardening etc. as per APPCB Norms.

20. Provide Fire resistant swing door For the collapsible life in all doors Provide Generator, as alternate Source of electric supply. Emergency Lighting in the corridors/common Passage and stair cases

For METROPOLITAN COMMISSIONER Hyderabad Metropolitan Development Authority

OWNER'S SIGN For Namishree Projects Partner

BUILDER'S SIGN For Namishree Infrastructure & Projects Pvt. Ltd. Managing Director

STRUCTURAL CONSULTANT

ARCHITECT For Namishree Projects Partner

Scale : As indicated Date : 18-07-2023

CLUBHOUSE FLOOR PLAN & SECTION