



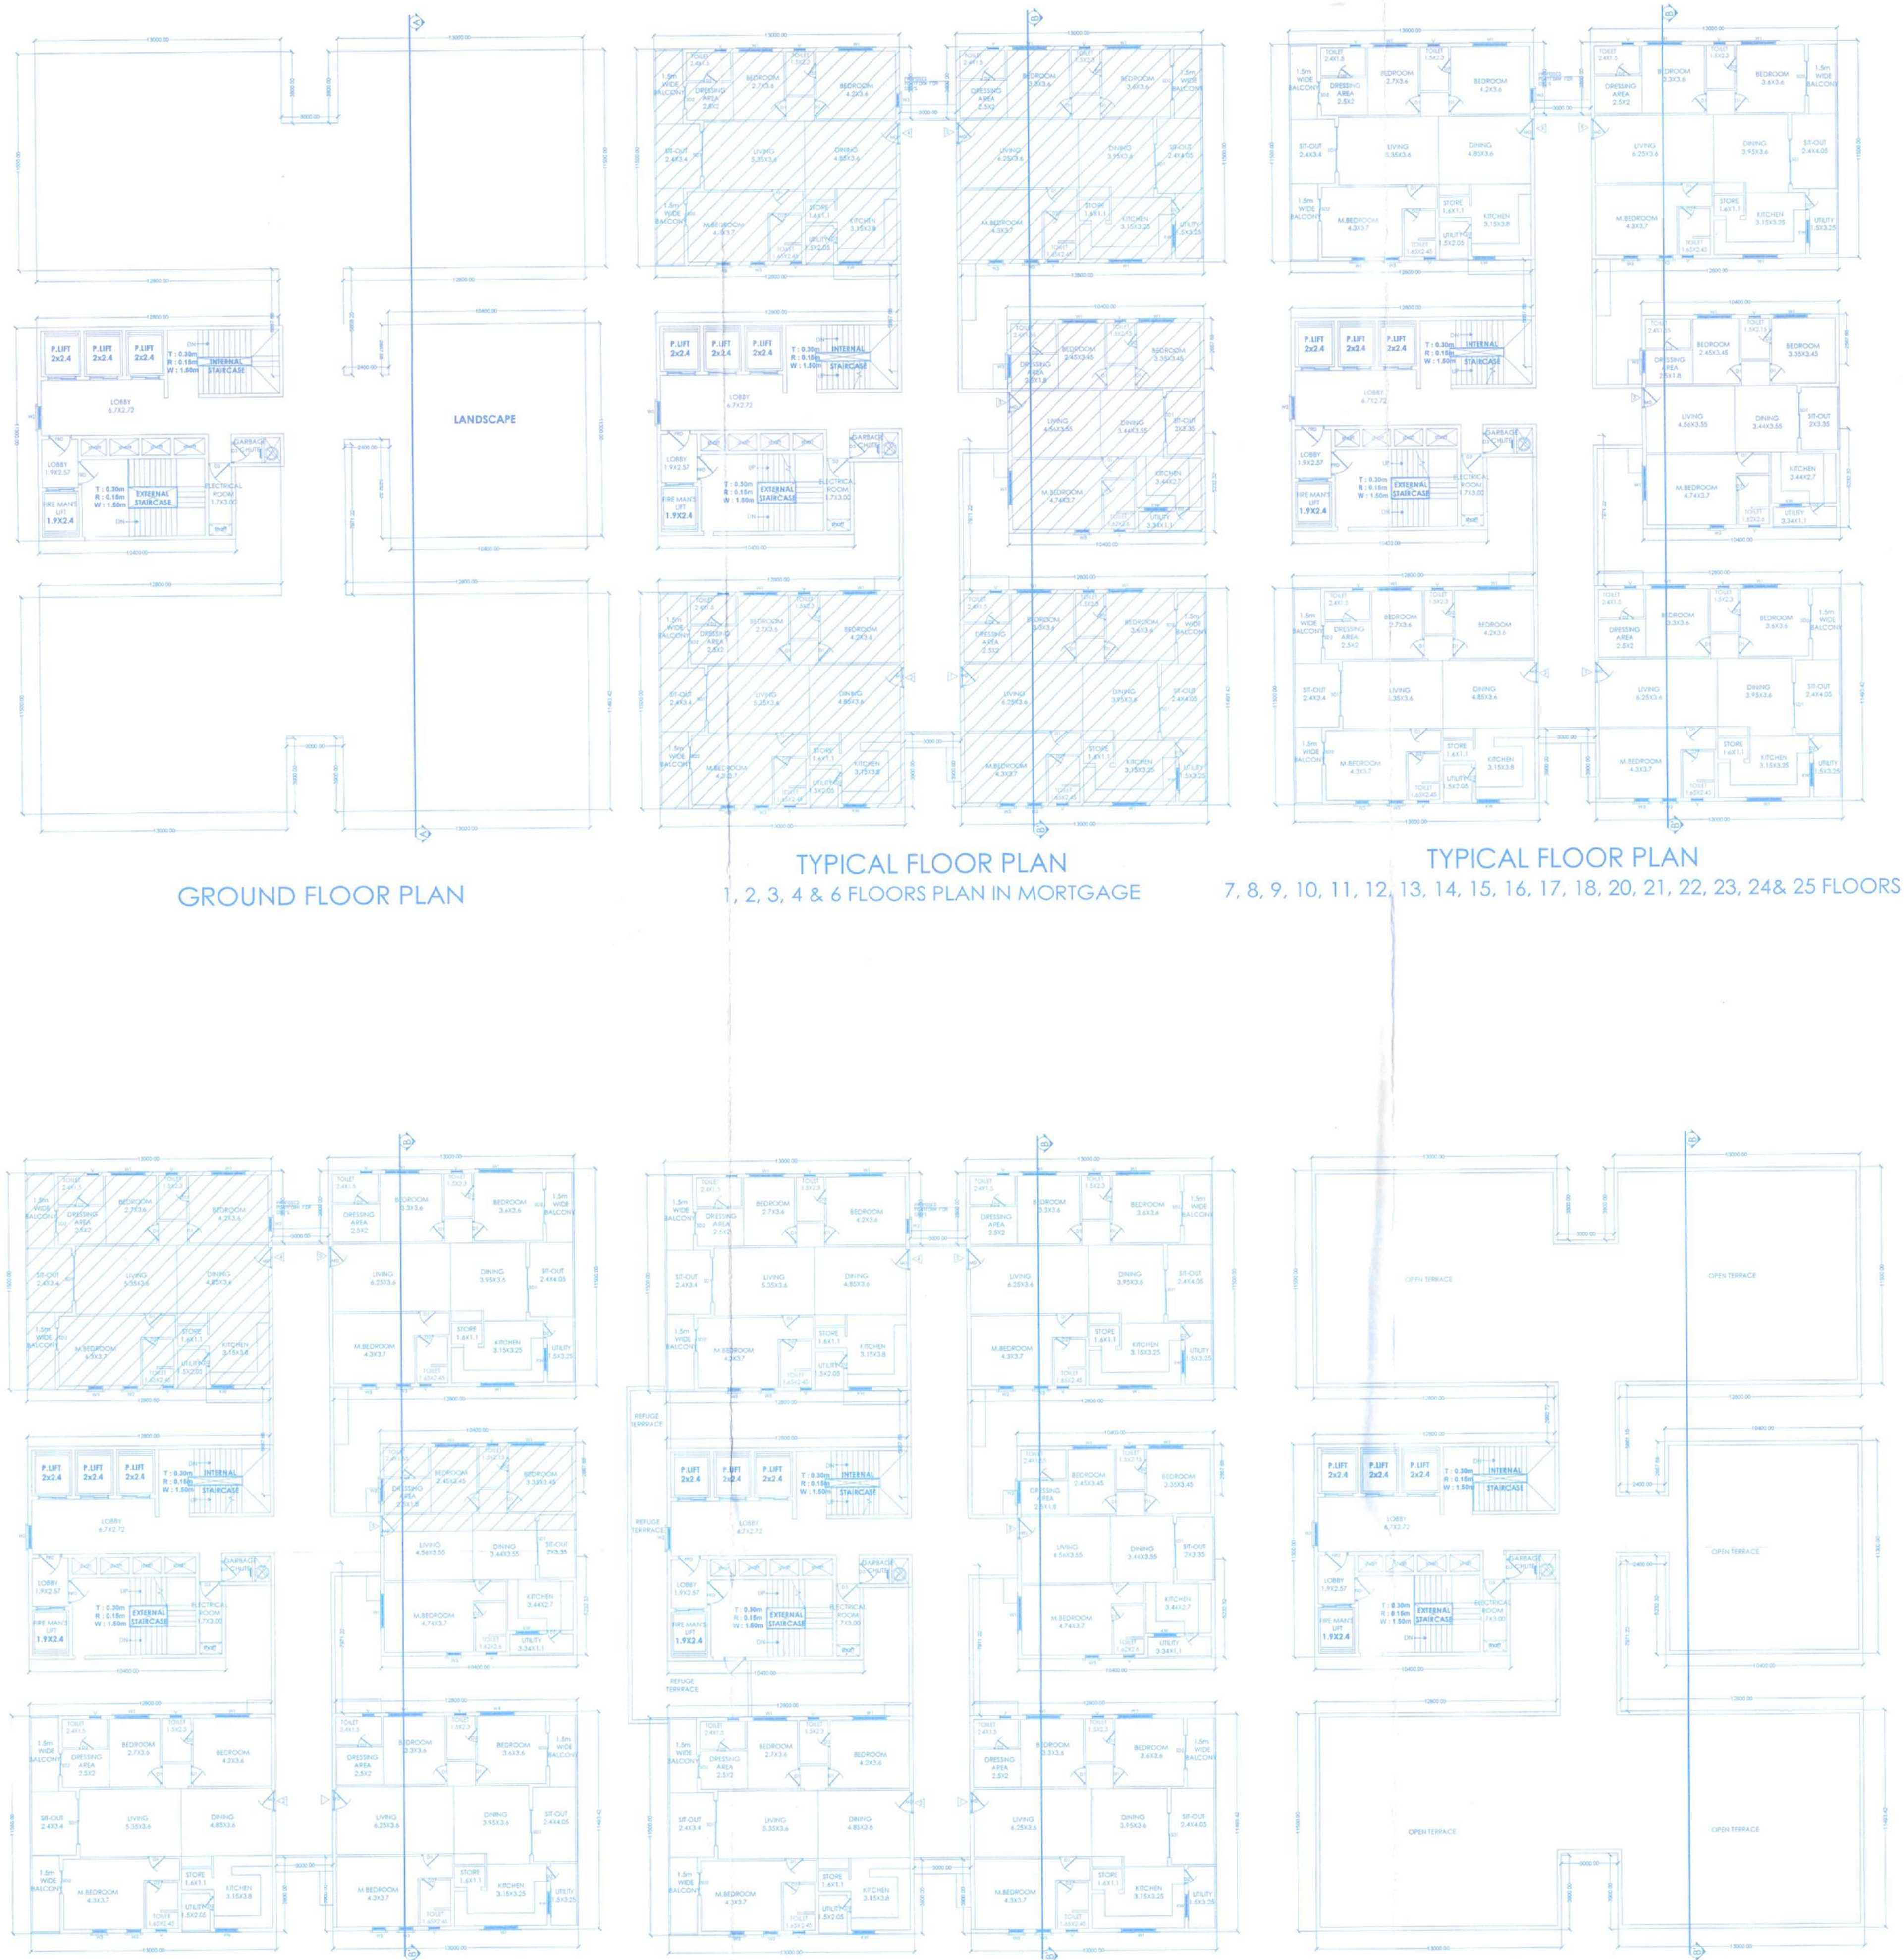

FIFTH FLOOR PLAN IN MORTGAGE

NINETEENTH FLOOR PLAN

TERRACE PLAN

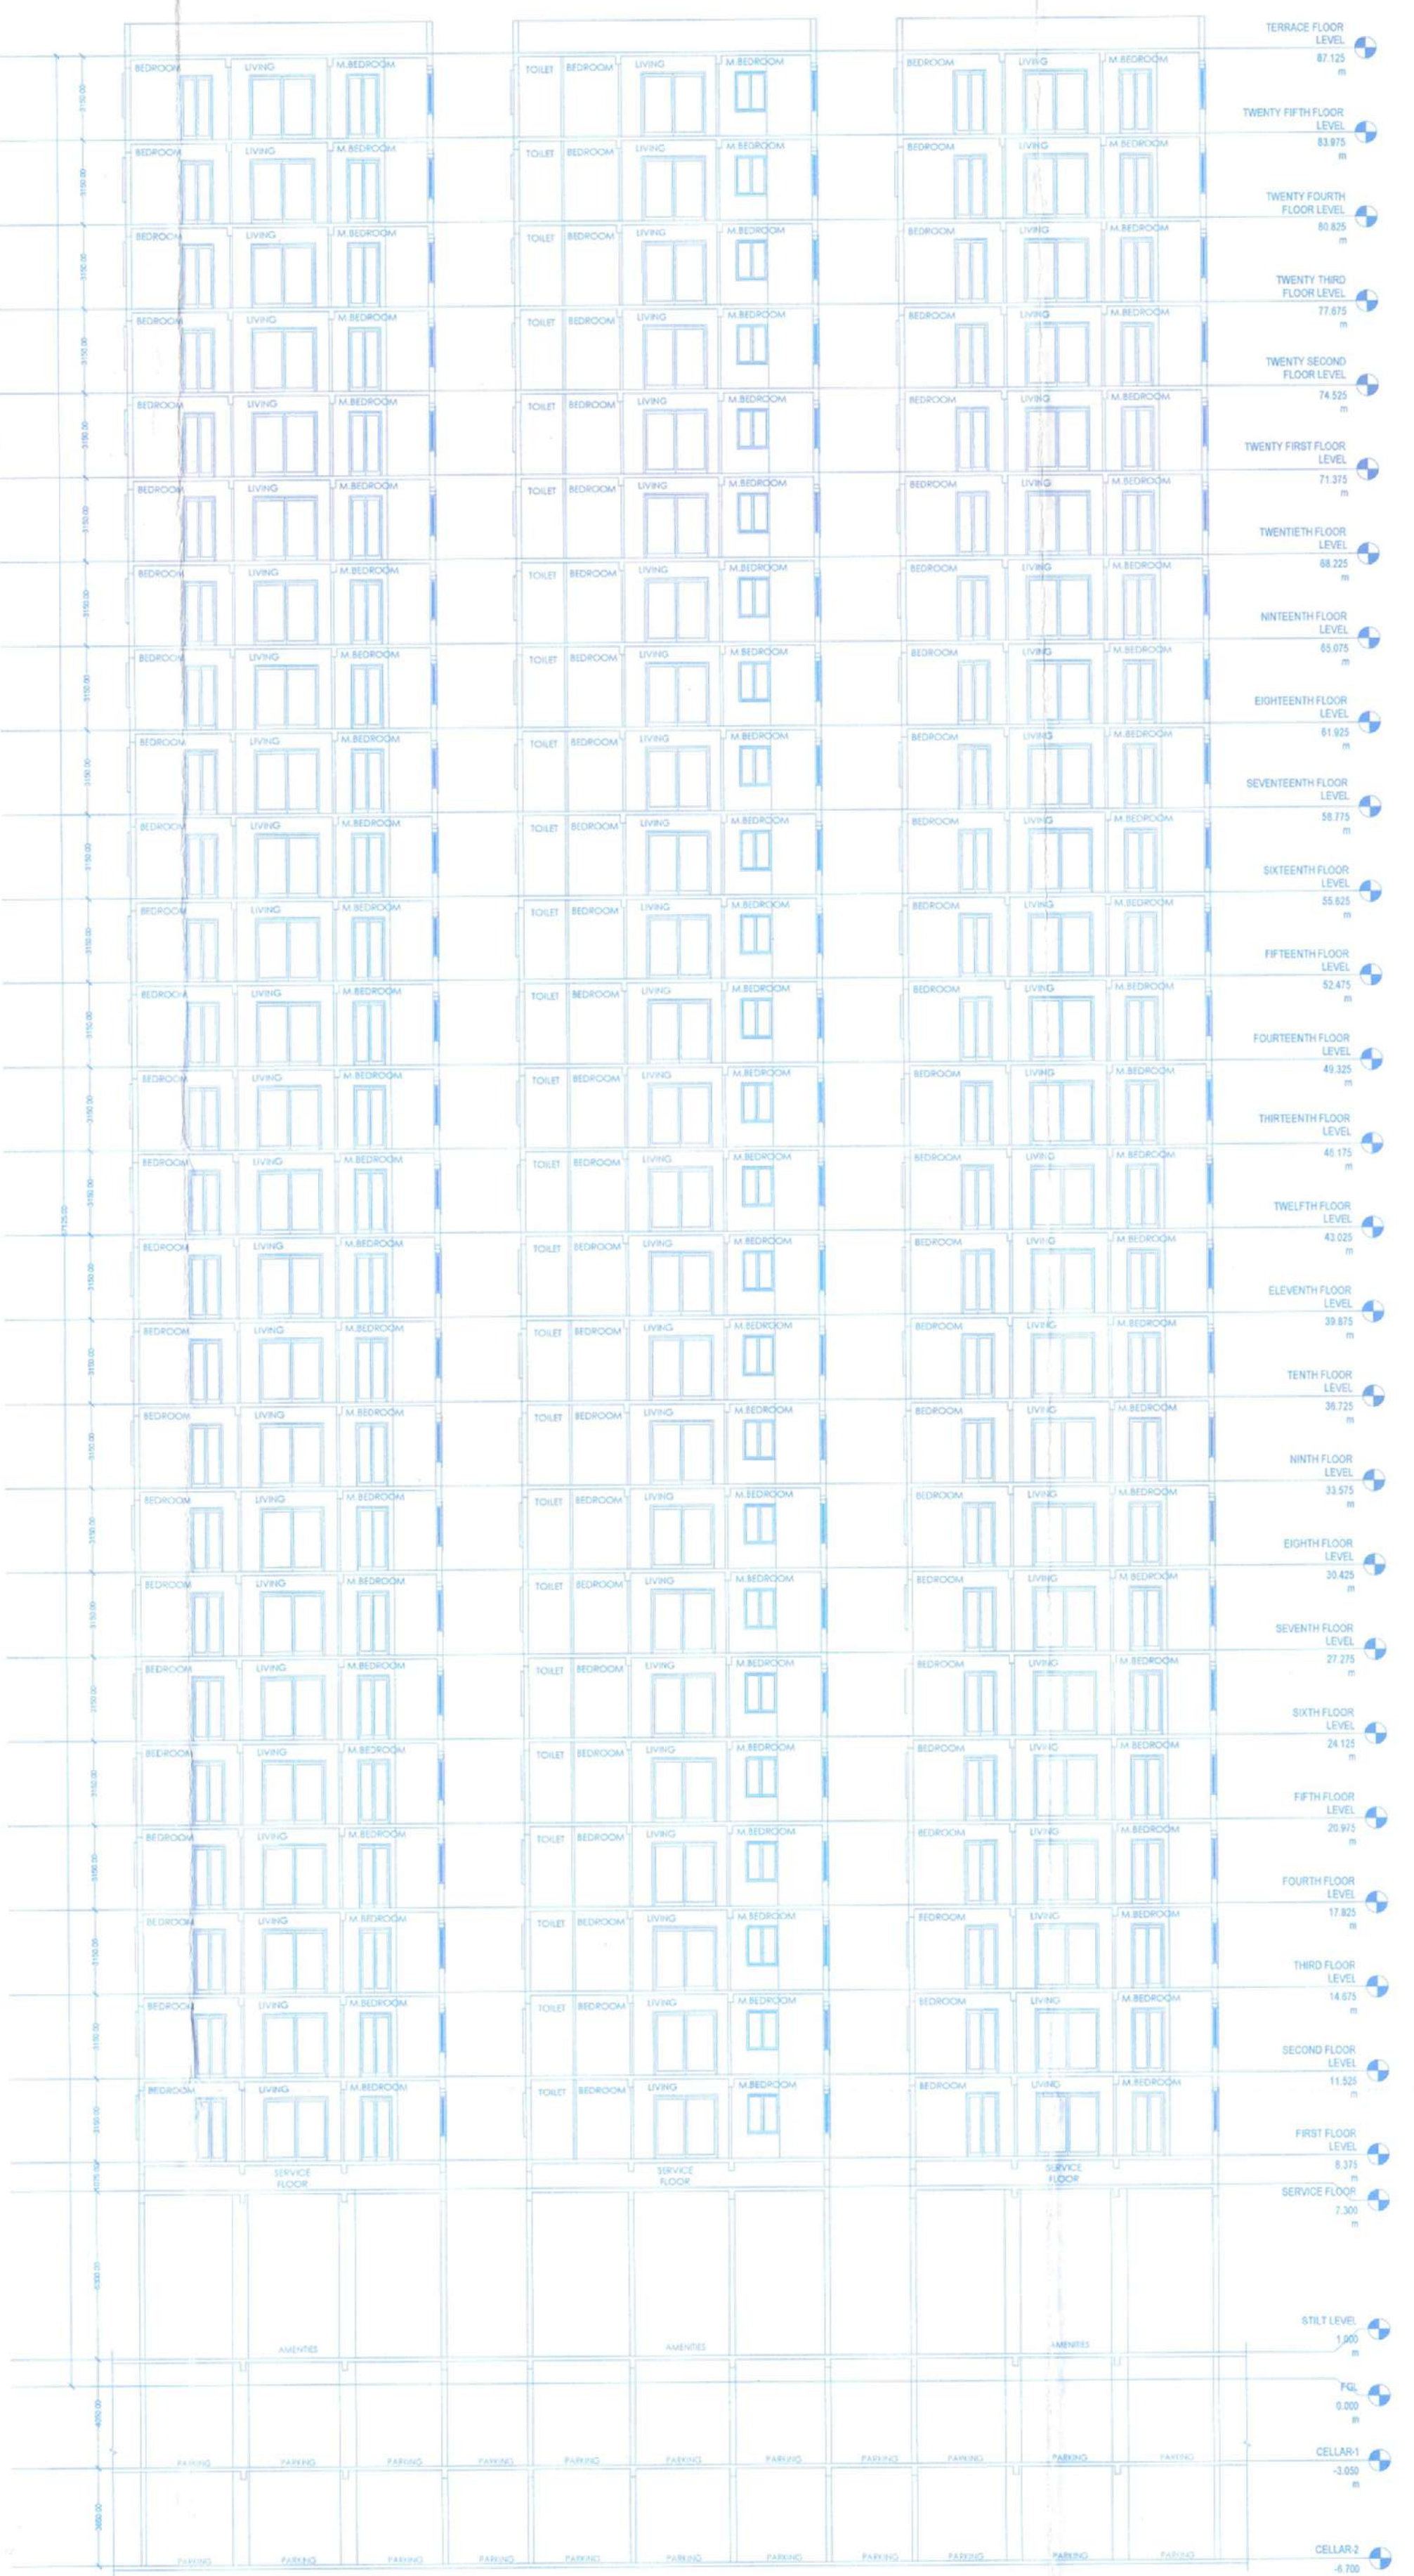

SECTION - BB'

TYPICAL BLOCK - D & E FLOOR PLANS

TECHNICAL APPROVAL IS HERE BY ACCORDED FOR ONLY DWELLING UNITS UNDER SECTION 20(2) 1. II OF HYDERABAD METROPOLITAN DEVELOPMENT AUTHORITY ACT 2002 & FORWARDED TO THE MUNICIPALITY/LOCAL BODY FOR FINAL SANCTION SUBJECT TO CONDITIONS MENTIONED ON APPROVED PLAN. CORRECTED DT: 10.10.2023. 06/10/2023/MD/23/11/197/MA/18-5-47

- This approval does not bar the application of the provision of the Urban Land (Ceiling & Regulation) Act, 1976.
- The local authority shall ensure that ownership clearance (and Urban Land Ceiling/clearance of the site under reference are in order and should scrupulously follow the Government instructions vide Memo No. 19333/1/11/97 MA, dt: 18-5-97 before sanctioning and releasing these technical approved building plans.
- This approval does not center or attempt the ownership of the site. Authority of ownership site boundary is the responsibility of the applicant.
- The Builder/Developer/Owner shall be responsible and ensure the five safety structural stability requirements of the proposed complex are in accordance with the National Building Code, 2005 provisions.
- The Commissioner of Municipality/Local Authority should physically take over the land shown in Road widening at free of cost before releasing Building permission as per statutory Master Plan/Z.D.F.
- The Car/Shift parking should not be mis-used for any other purpose.
- The Builder/Developer should conform and dump, drainage as per ISI Standards and to the satisfaction of Municipality in addition to the drainage system available.
10. THAT THE APPLICANT SHALL COMPLY THE CONDITIONS Laid down G.O.M.S. NO. 470 M.A. Dt: 8-7-2008, G.O.M.S. NO. 168 M.A. Dt: 7-4-2017 AND ITS ENFORCEMENTS.
11. The applicant shall comply with the A.P. FIRE SERVICES ACT, 1999.
12. This permission does not give any right of public agency include HMDA/Local Body to acquire the lands for public purpose as per Law.
13. Two numbers water type fire extinguisher Per every 600 Sq.Mtrs of floor area with Minimum of four numbers fire extinguisher Per floor and 5 kg. DCP extinguisher minimum 2 Nos. each at Generator and Transformer area shall be provided as per alarm ISI specification No.2190-1992.
14. Manually operated fire alarm system in the Entire Building; Separate Underground static Water storage tank capacity of 25,000 Lts. capacity Separate Terrace tank of 25,000 Lts. capacity for Residential Buildings; House Riser from C.M.
15. Automatic Sprinkler system is to be provided if the basement area exceeds 200 Sq. Mtrs. Electrical wiring and installation shall be Certified by the electrical engineers to ensure electrical fire safety.
16. To create a joint open spaces with the Neighbour building / premises for Manoeuvrability of fire vehicles. No parking. Or any constructions shall be made in setbacks area.
17. Transformers shall be provided with 4 hours Rating fire resistant construction as per Rule 15(e) of A.P. Apartments (Promotion) of construction and owners 1987.
18. To provide one entry and on out. To the premises with a minimum Width of 4.5 mtrs and height Clearance of 5 mtrs.
19. To provide sewage disposal, gas or reception Of sewage water for disposal and solid waste for Gardening etc. as per APCCB norms.
20. Provide Fire resistant using UOOD For the collapsible life in all doors. Provide Generator, as alternate Source of electricity. Emergency Lightening, the corridors/entrance Passage and stair cases.

For METROPOLITAN COMMISSIONER Hyderabad Metropolitan Development Authority

PLANS		SHEET NO. 5, TOTAL No. OF SHEETS : 6	
PLAN SHOWING THE PROPOSED CONSTRUCTION OF RESIDENTIAL APARTMENT IN SY.NO.121/PART. SITUATED AT TATIANARAM VILLAGE, ABULAPURMET MANDAL, (PREVIOUSLY KNOWN AS HAYATHNAGAR MANDAL, RANGA REDDY DISTRICT.			
BELONGING TO:			
SRI C. AMARENDER REDDY & OTHERS REPRESENTED BY THEIR GPO HOLDER 'NAMISHREE PROJECTS' REPRESENTED BY SRI. MOTILAL JAIN			
SCHEDULE OF OPENINGS			
MAIN DOOR (MD)		1.07M X 2.4M	
SINGLE FLUSH DOOR (D1)		0.90M X 2.1M	
SINGLE FLUSH DOOR (D2)		0.75M X 2.1M	
SINGLE FLUSH DOOR (D3)		1.10M X 2.1M	
SLIDING DOOR (SD1)		2.40M X 2.4M	
SLIDING DOOR (SD2)		1.20M X 2.4M	
FIRE DOOR (FD)		1.20M X 2.4M	
SLIDING WINDOW (W1)		1.83M X 1.50M	
SLIDING WINDOW (W2)		1.20M X 1.50M	
SLIDING WINDOW (W3)		0.75M X 1.20M	
SLIDING WINDOW (W4)		1.20M X 1.50M	
VENTILATOR (V)		0.60M X 1.20M	
AREA STATEMENT			
TOTAL LAND AREA 6.15 ACRES (OR) 26789.18 SYD (OR) 24607.34 SMT			
ROAD WIDENING AREA : 65.97 SYD (OR) 80.24 SMT			
NET LAND AREA : 29693.21 SYD (OR) 24827.10 SMT			
BLOCK A			
GROUND FLOOR		128.42 SMT	
TYPICAL FLOOR AREA		955.02 SMT X 24 = 22,920.48 SMT	
NINETEENTH FLOOR AREA		1004.51 SMT	
TOTAL BUILT-UP AREA		24,053.71 SMT	
BLOCK B			
GROUND FLOOR		128.42 SMT	
TYPICAL FLOOR AREA		955.02 SMT X 24 = 22,920.48 SMT	
NINETEENTH FLOOR AREA		1004.51 SMT	
TOTAL BUILT-UP AREA		24,053.71 SMT	
BLOCK C			
GROUND FLOOR		128.42 SMT	
TYPICAL FLOOR AREA		955.02 SMT X 24 = 22,920.48 SMT	
NINETEENTH FLOOR AREA		1004.51 SMT	
TOTAL BUILT-UP AREA		24,053.71 SMT	
BLOCK D			
GROUND FLOOR		128.42 SMT	
TYPICAL FLOOR AREA		955.02 SMT X 24 = 22,920.48 SMT	
NINETEENTH FLOOR AREA		1004.51 SMT	
TOTAL BUILT-UP AREA		24,053.71 SMT	
BLOCK E			
GROUND FLOOR		128.42 SMT	
TYPICAL FLOOR AREA		955.02 SMT X 24 = 22,920.48 SMT	
NINETEENTH FLOOR AREA		1004.51 SMT	
TOTAL BUILT-UP AREA		24,053.71 SMT	
TOTAL AREA (BLOCKS A, B, C, D & E) : 1,20,269.51 SMT			
AMENITIES BLOCK AREA REQUIRED 3% OF 1,20,269.51 = 3608.08 SMT			
AMENITIES BLOCK AREA PROVIDED : 6085.01 SMT			
PARKING AREA REQUIRED			
PARKING AREA REQUIRED (RESIDENTIAL) : 22% = 28467.27 SMT			
PARKING AREA PROVIDED : 37236.70 SMT			
CELLAR FLOOR AREA : 18733.60 SMT			
SUB CELLAR FLOOR AREA : 18503.10 SMT			
VENTILATION REQUIRED 2.5% OF CELLAR AREA : 469.71 SMT			
VENTILATION PROVIDED OF CELLAR AREA : 547.04 SMT			
TOT LOT REQUIRED 10% OF NET LAND AREA : 2484.8745 SMT			
TOT LOT PROVIDED : 2527.07 SMT			
TOTAL NO OF UNITS: 625; LARGE UNITS=500, SMALL UNITS=125			
TOTAL NO OF CARS:			
BASEMENT-1=466 NOS			
BASEMENT-2=466 NOS			
SURFACE PARKING=119 NOS			
TOTAL NO OF CARS (PROVIDED) = 1111 NOS			
10% MORTGAGE AREA REQUIRED : 12635.42 SMT			
5% MORTGAGE AREA REQUIRED : 6317.71 SMT			
TOTAL MORTGAGE AREA REQUIRED : 18953.13 SMT			
TOTAL MORTGAGE AREA PROVIDED : 18204.50 SMT			
TOTAL NO OF FLOORS			
BLOCK A, B, C, D & E - SUB CELLAR-CELLAR-GROUND-25 FLOORS			
OWNER'S SIGN			
For NAMISHREE PROJECTS SRI. MOTILAL JAIN Partner			
BUILDER'S SIGN			
For Namishree Infrastructure & Projects Pvt. Ltd. SRI. MOTILAL JAIN Authorized Signatory			
STRUCTURAL CONSULTANT			
ARCHITECT			
Scale : As indicated			
Date : 10/01/23			
FLOOR PLANS WITH SECTION & ELEVATION - TYPE B			